



www.autodesk.com/revit


Consultant
Address
Address
Phone
Fax
e-mail

Consultant
Address
Address
Phone
Fax
e-mail


Consultant
Address
Address
Phone
Fax
e-mail

Consultant
Address
Address
Phone
Fax
e-mail

Consultant
Address
Address
Phone
Fax
e-mail

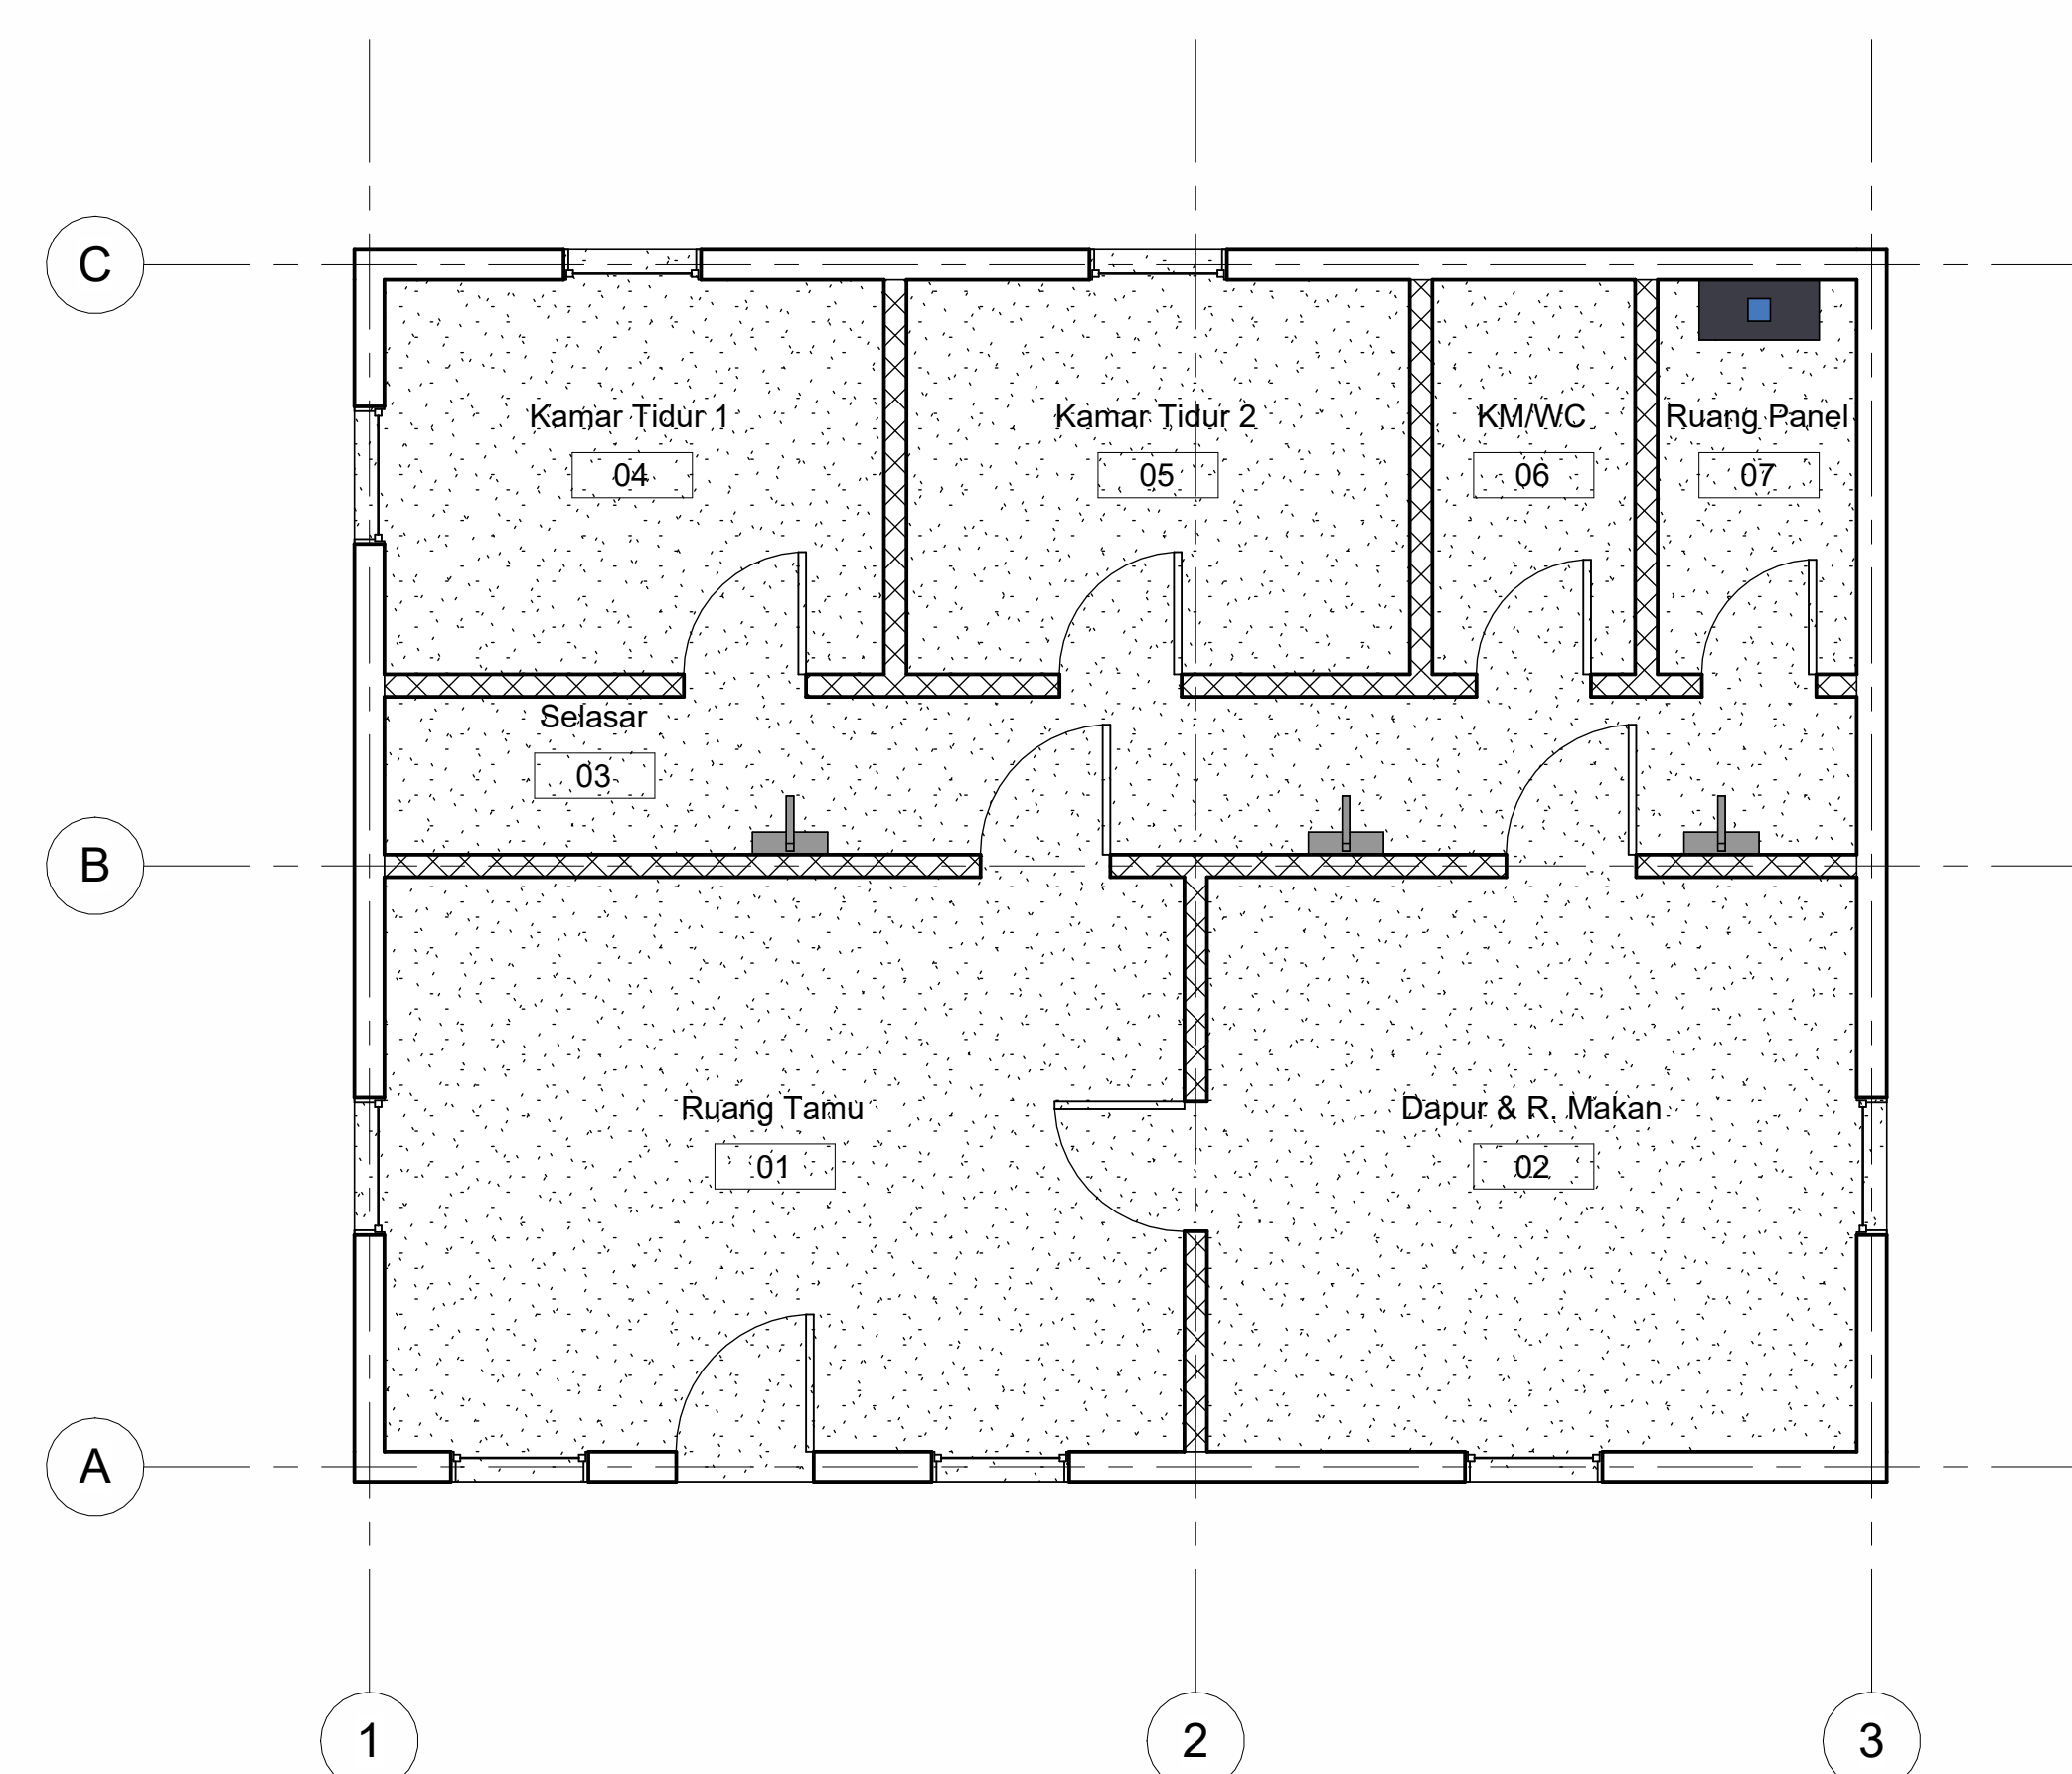

1 Denah Arsitektur - Lantai 1
1 : 50

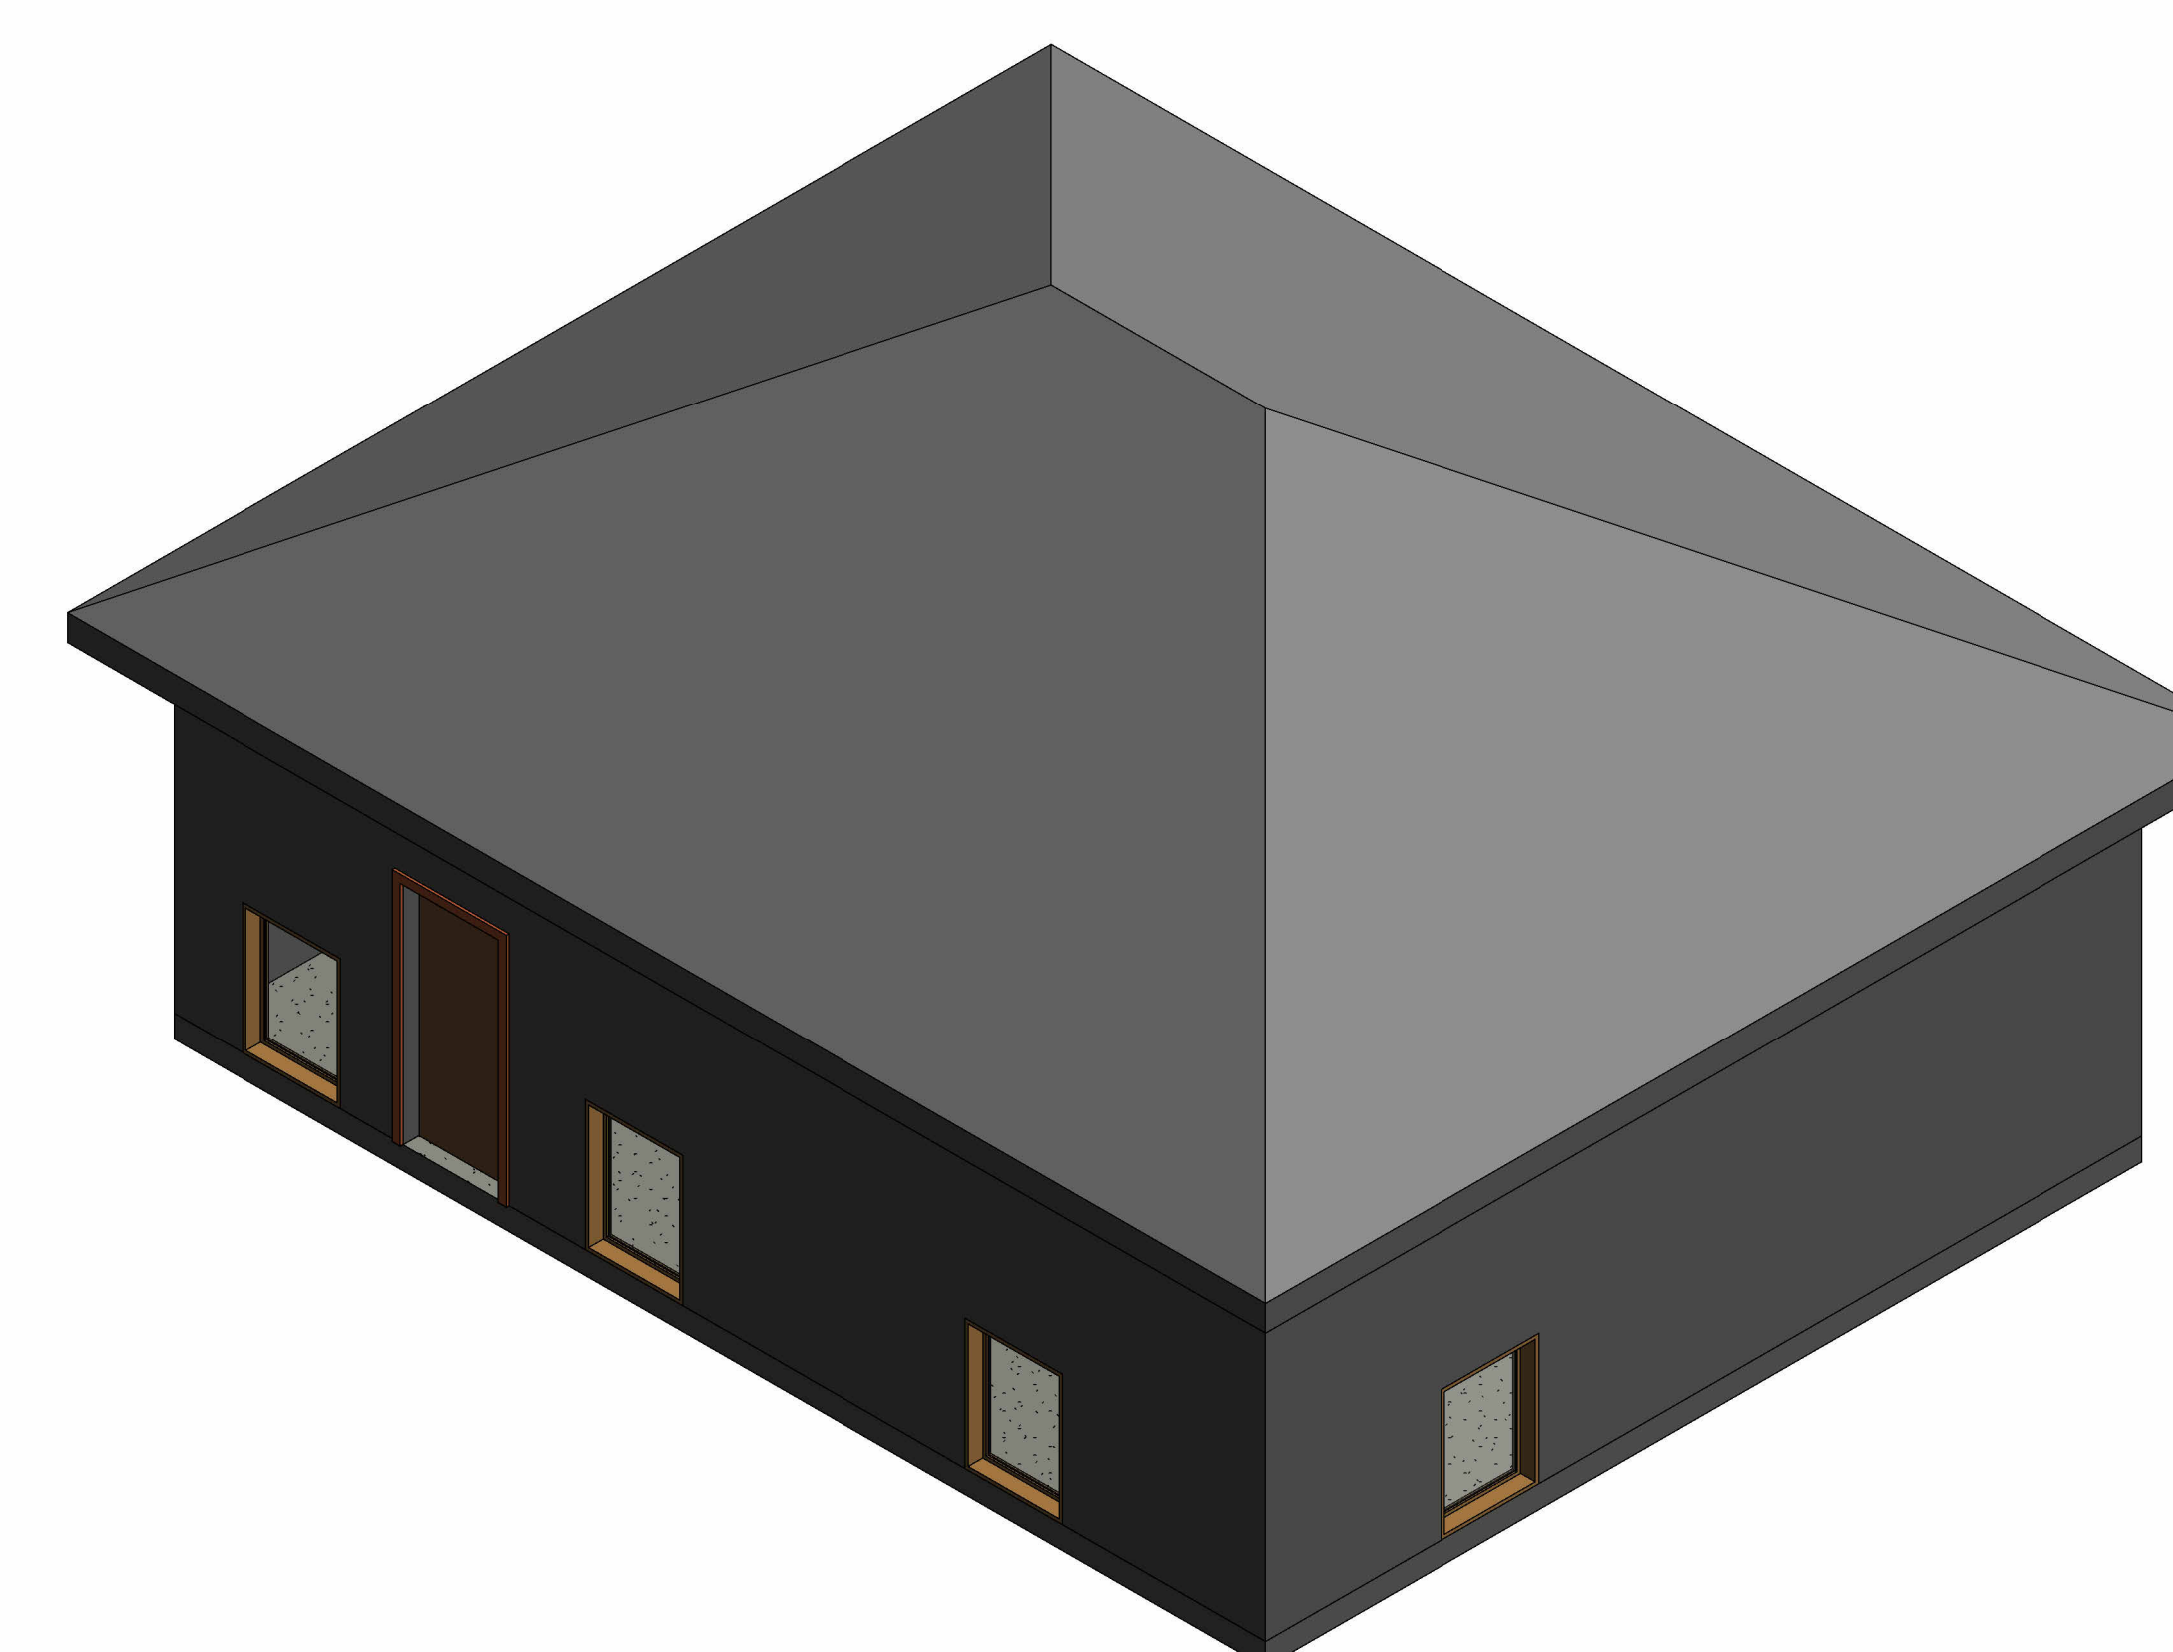

2 3D - Rumah

[illegible]

Rumah
Sederhana +
Sablq
Skema
Busduct

Denah & 3D Rumah

Project number	RS-BD-001
----------------	-----------



Date	24-09-2026
------	------------

Drawn by Claude

Checked by	Checker
------------	---------

A-101

Scale	1 : 50
-------	--------

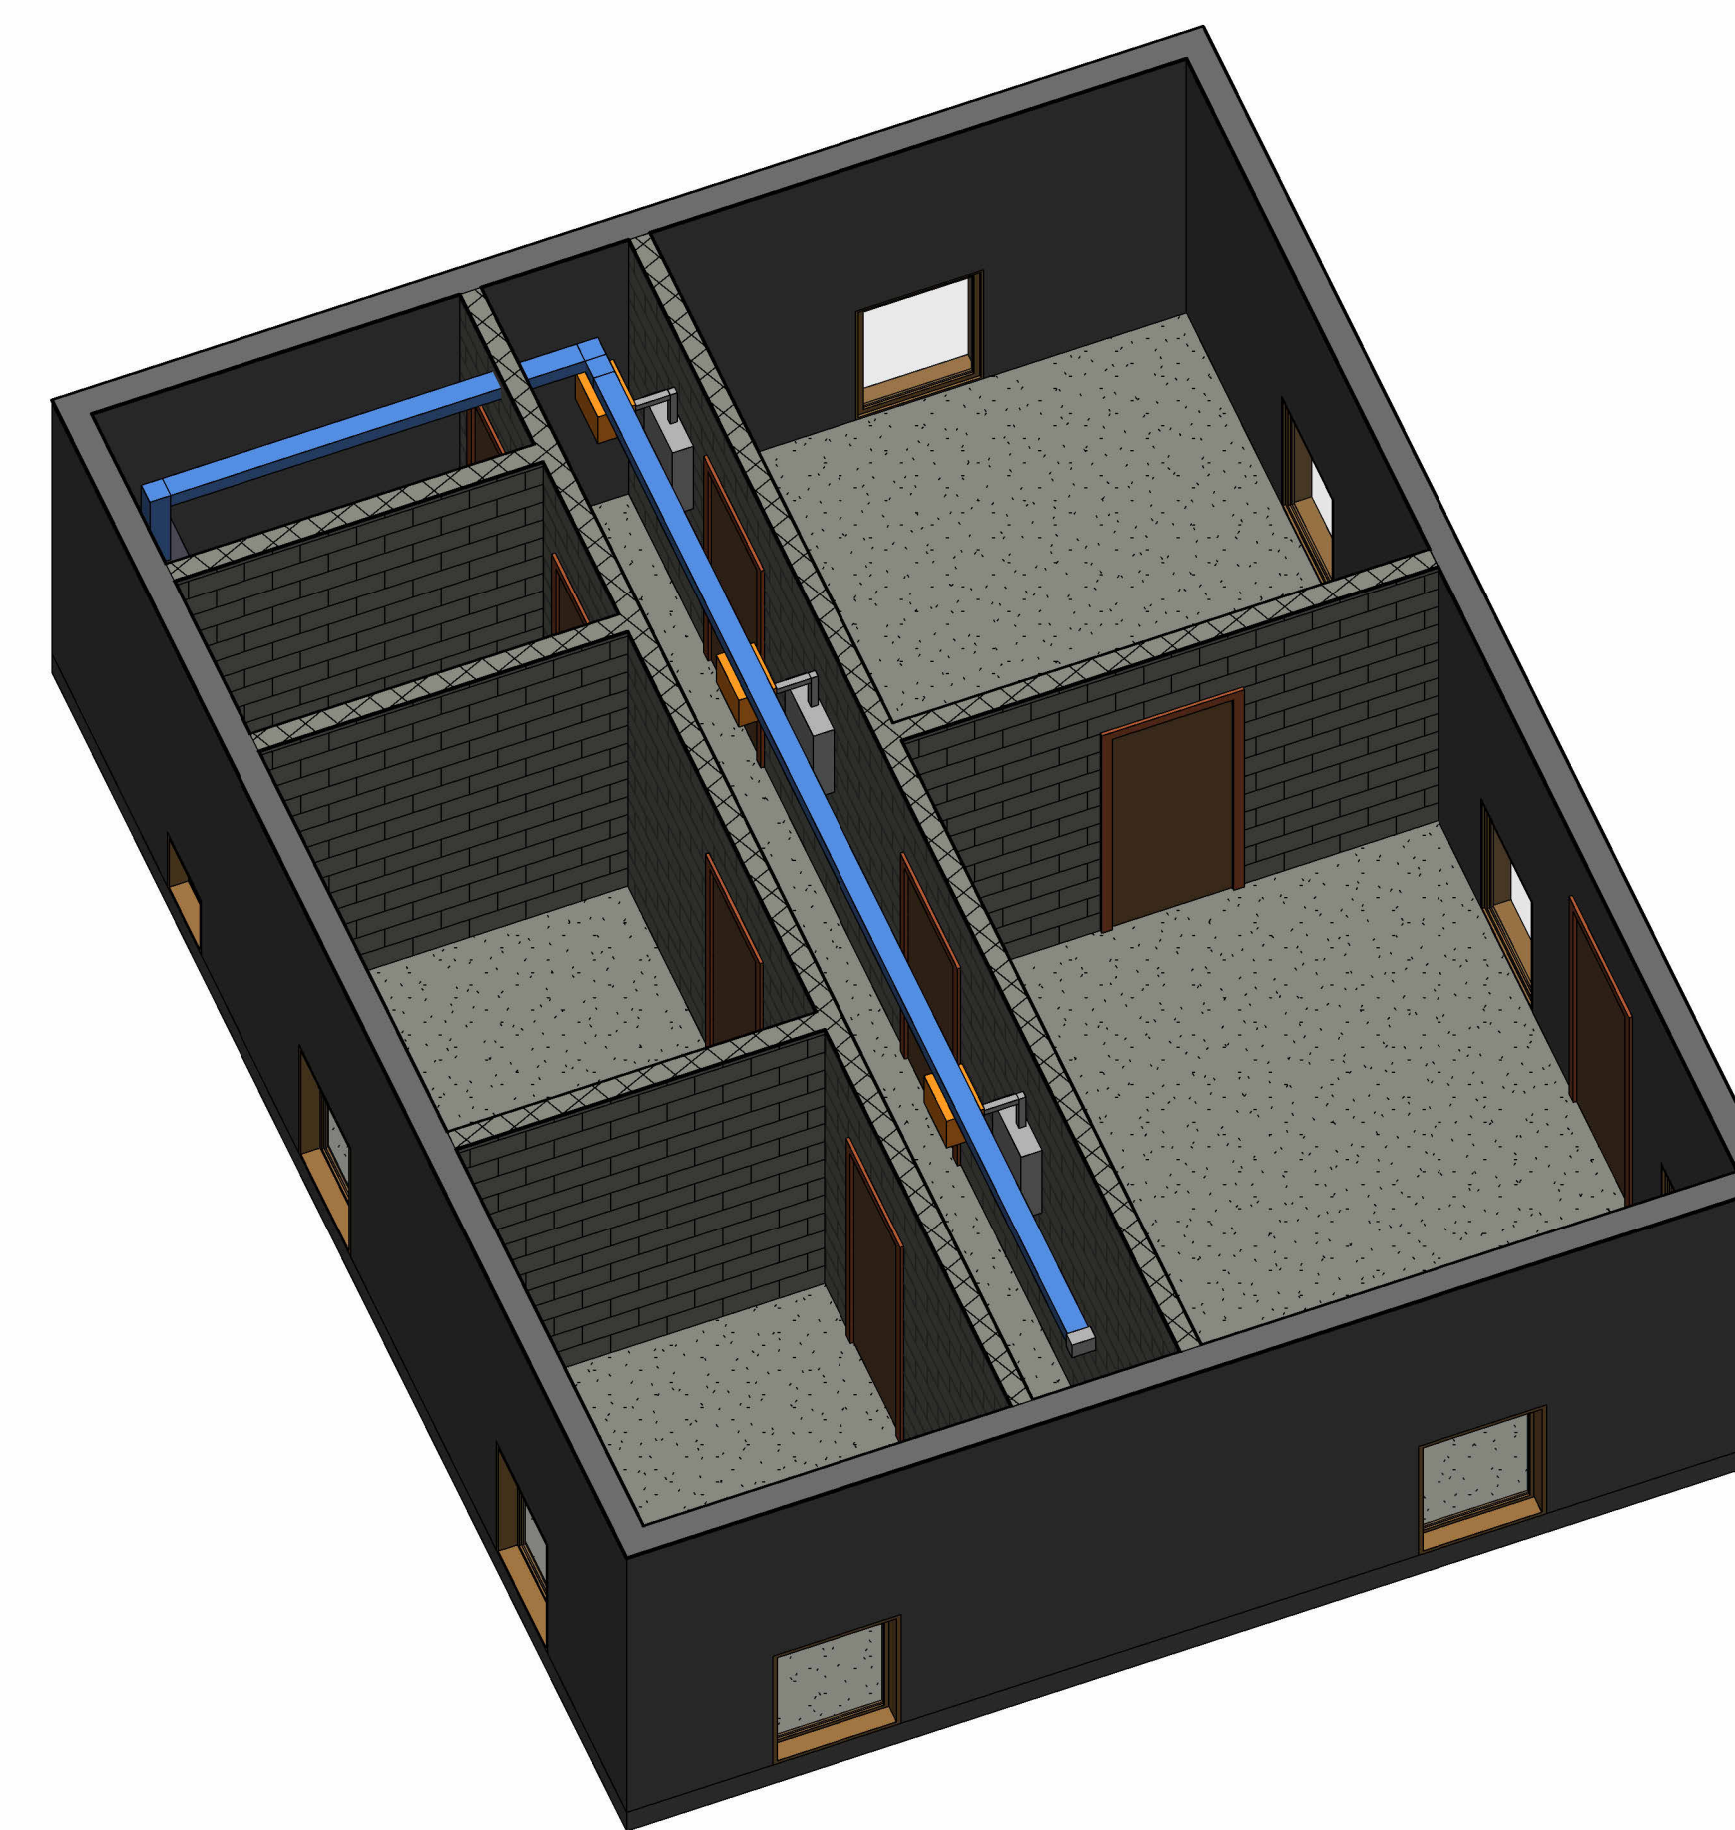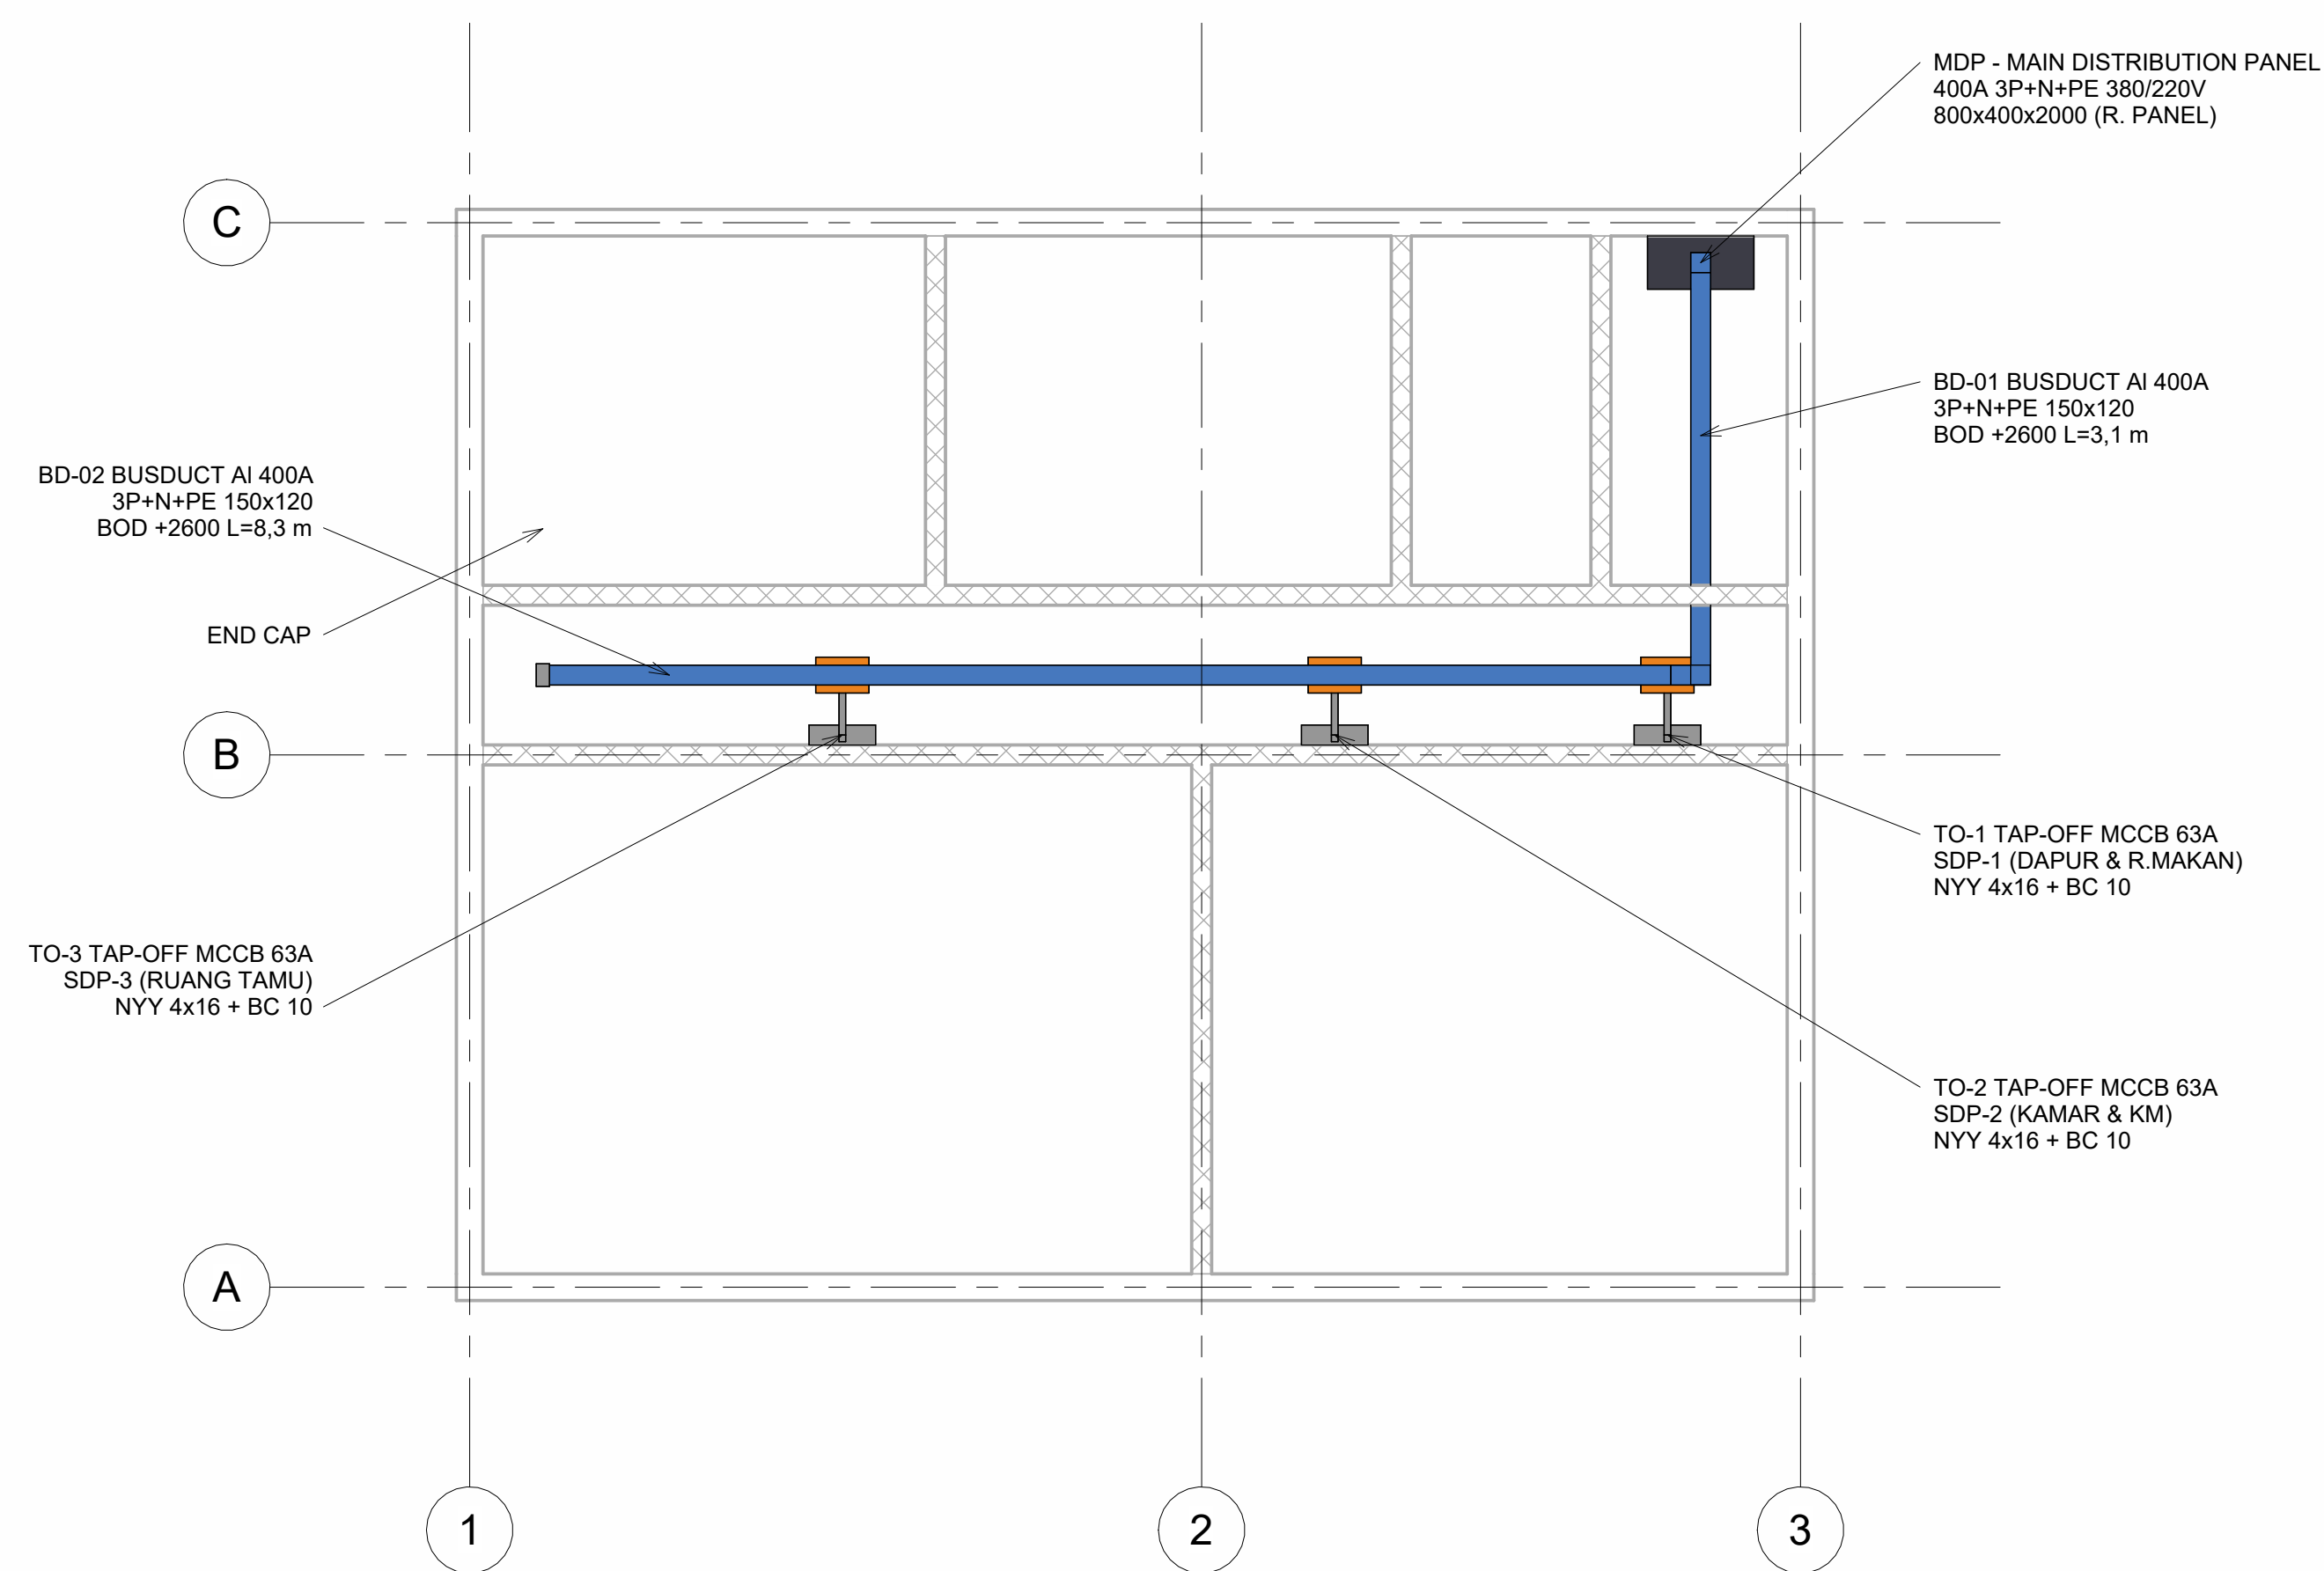

Jadwal Peralatan Busduct	
KODE	SPEKIFIKASI
BD-01	Busduct AI 400A 3P+N+PE (5 konduktor), 150x120, BOD +2600, L=3,1 m
BD-02	Busduct AI 400A 3P+N+PE, 150x120, BOD +2600, L=8,3 m
BD-EC	End closure 400A
BD-EL1	Elbow horizontal 90 deg 400A
BD-FU	Flange end feed unit 400A
FD-1	NY Y 4x16mm ² + BC 10mm ² dalam flexible conduit
FD-2	NY Y 4x16mm ² + BC 10mm ² dalam flexible conduit
FD-3	NY Y 4x16mm ² + BC 10mm ² dalam flexible conduit
MDP	MDP 400A 3P+N+PE, 380/220V, IP54, 80x400x2000
SDP-1	Sub Distribution Panel 63A, wound mounted 500x150x700, BOD +1300
SDP-2	Sub Distribution Panel 63A, wall mounted 500x150x700, BOD +1300
SDP-3	Sub Distribution Panel 63A, wall mounted 500x150x700, BOD +1300
TO-1	Plug-in tap-off unit MCCB 63A 3P, feed ke SDP-1
TO-2	Plug-in tap-off unit MCCB 63A 3P, feed ke SDP-2
TO-3	Plug-in tap-off unit MCCB 63A 3P, feed ke SDP-3

Consultant
Address
Address
Phone
Fax
e-mail

Consultant
Address
Address
Phone
Fax
e-mail

Consultant
Address
Address
Phone
Fax
e-mail

Consultant
Address
Address
Phone
Fax
e-mail

Consultant
Address
Address
Phone
Fax
e-mail

[illegible]

Sederhana +
Sablq
Skema
Busduct

Skema Busduct 400A

Project number RS-BD-00

Date 24-09-202

Drawn by Claud

Checked by _____ Checked _____

E-101

Scale 1 : 5