




www.autodesk.com/revit

Consultant
Address
Address
Phone
Fax
e-mail

Consultant
Address
Address
Phone
Fax
e-mail

Consultant
Address
Address
Phone
Fax
e-mail


Consultant
Address
Address
Phone
Fax
e-mail

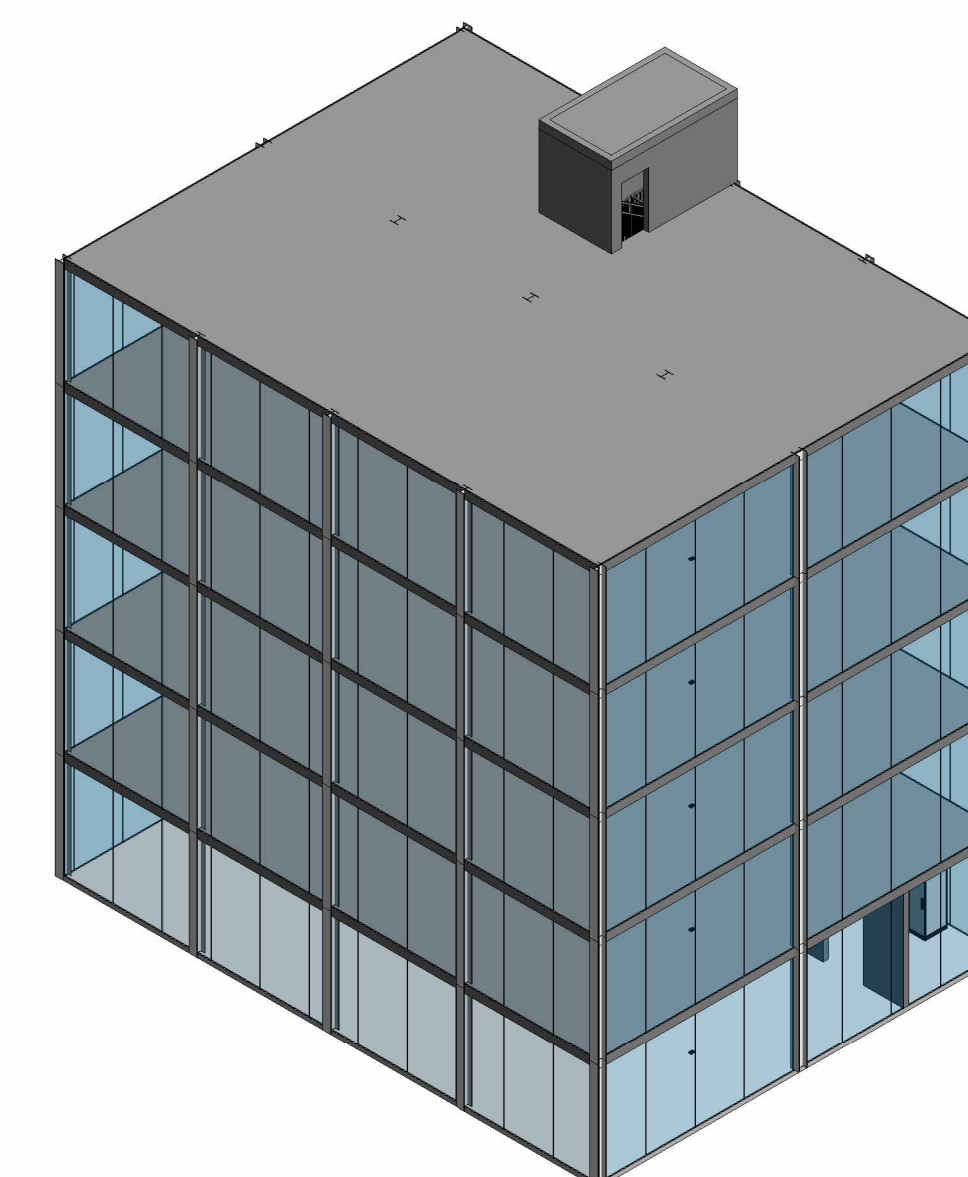

2 3D - Gedung 5 Lantai

LEGENDA SISTEM (GRAPHIC OVERRIDE)
 ORANYE : LV Busduct 800A Cu 4P+PE (3P+N+PE) 400/230V
 MERAH : LVMDP 1250A & DB-L1 s/d DB-L5 (250A)
 HIJAU : Feeder Cable Tray Tap-Off -> DB
 BIRU : Branch Cable Tray DB -> Beban
 UNGU : Beban (Lighting, Socket Outlet, AHU/HVAC)
 ABU-ABU (half tone) : Arsitektur & Struktur

ALUR DISTRIBUSI:
 Trafo -> LVMDP -> Busduct Horizontal (BD-H01) -> Elbow ->
 Vertical Busduct Riser (BD-R01..R05) -> Tap-Off (TO-Lx) ->
 Feeder Tray -> DB-Lx -> Branch Tray -> Beban

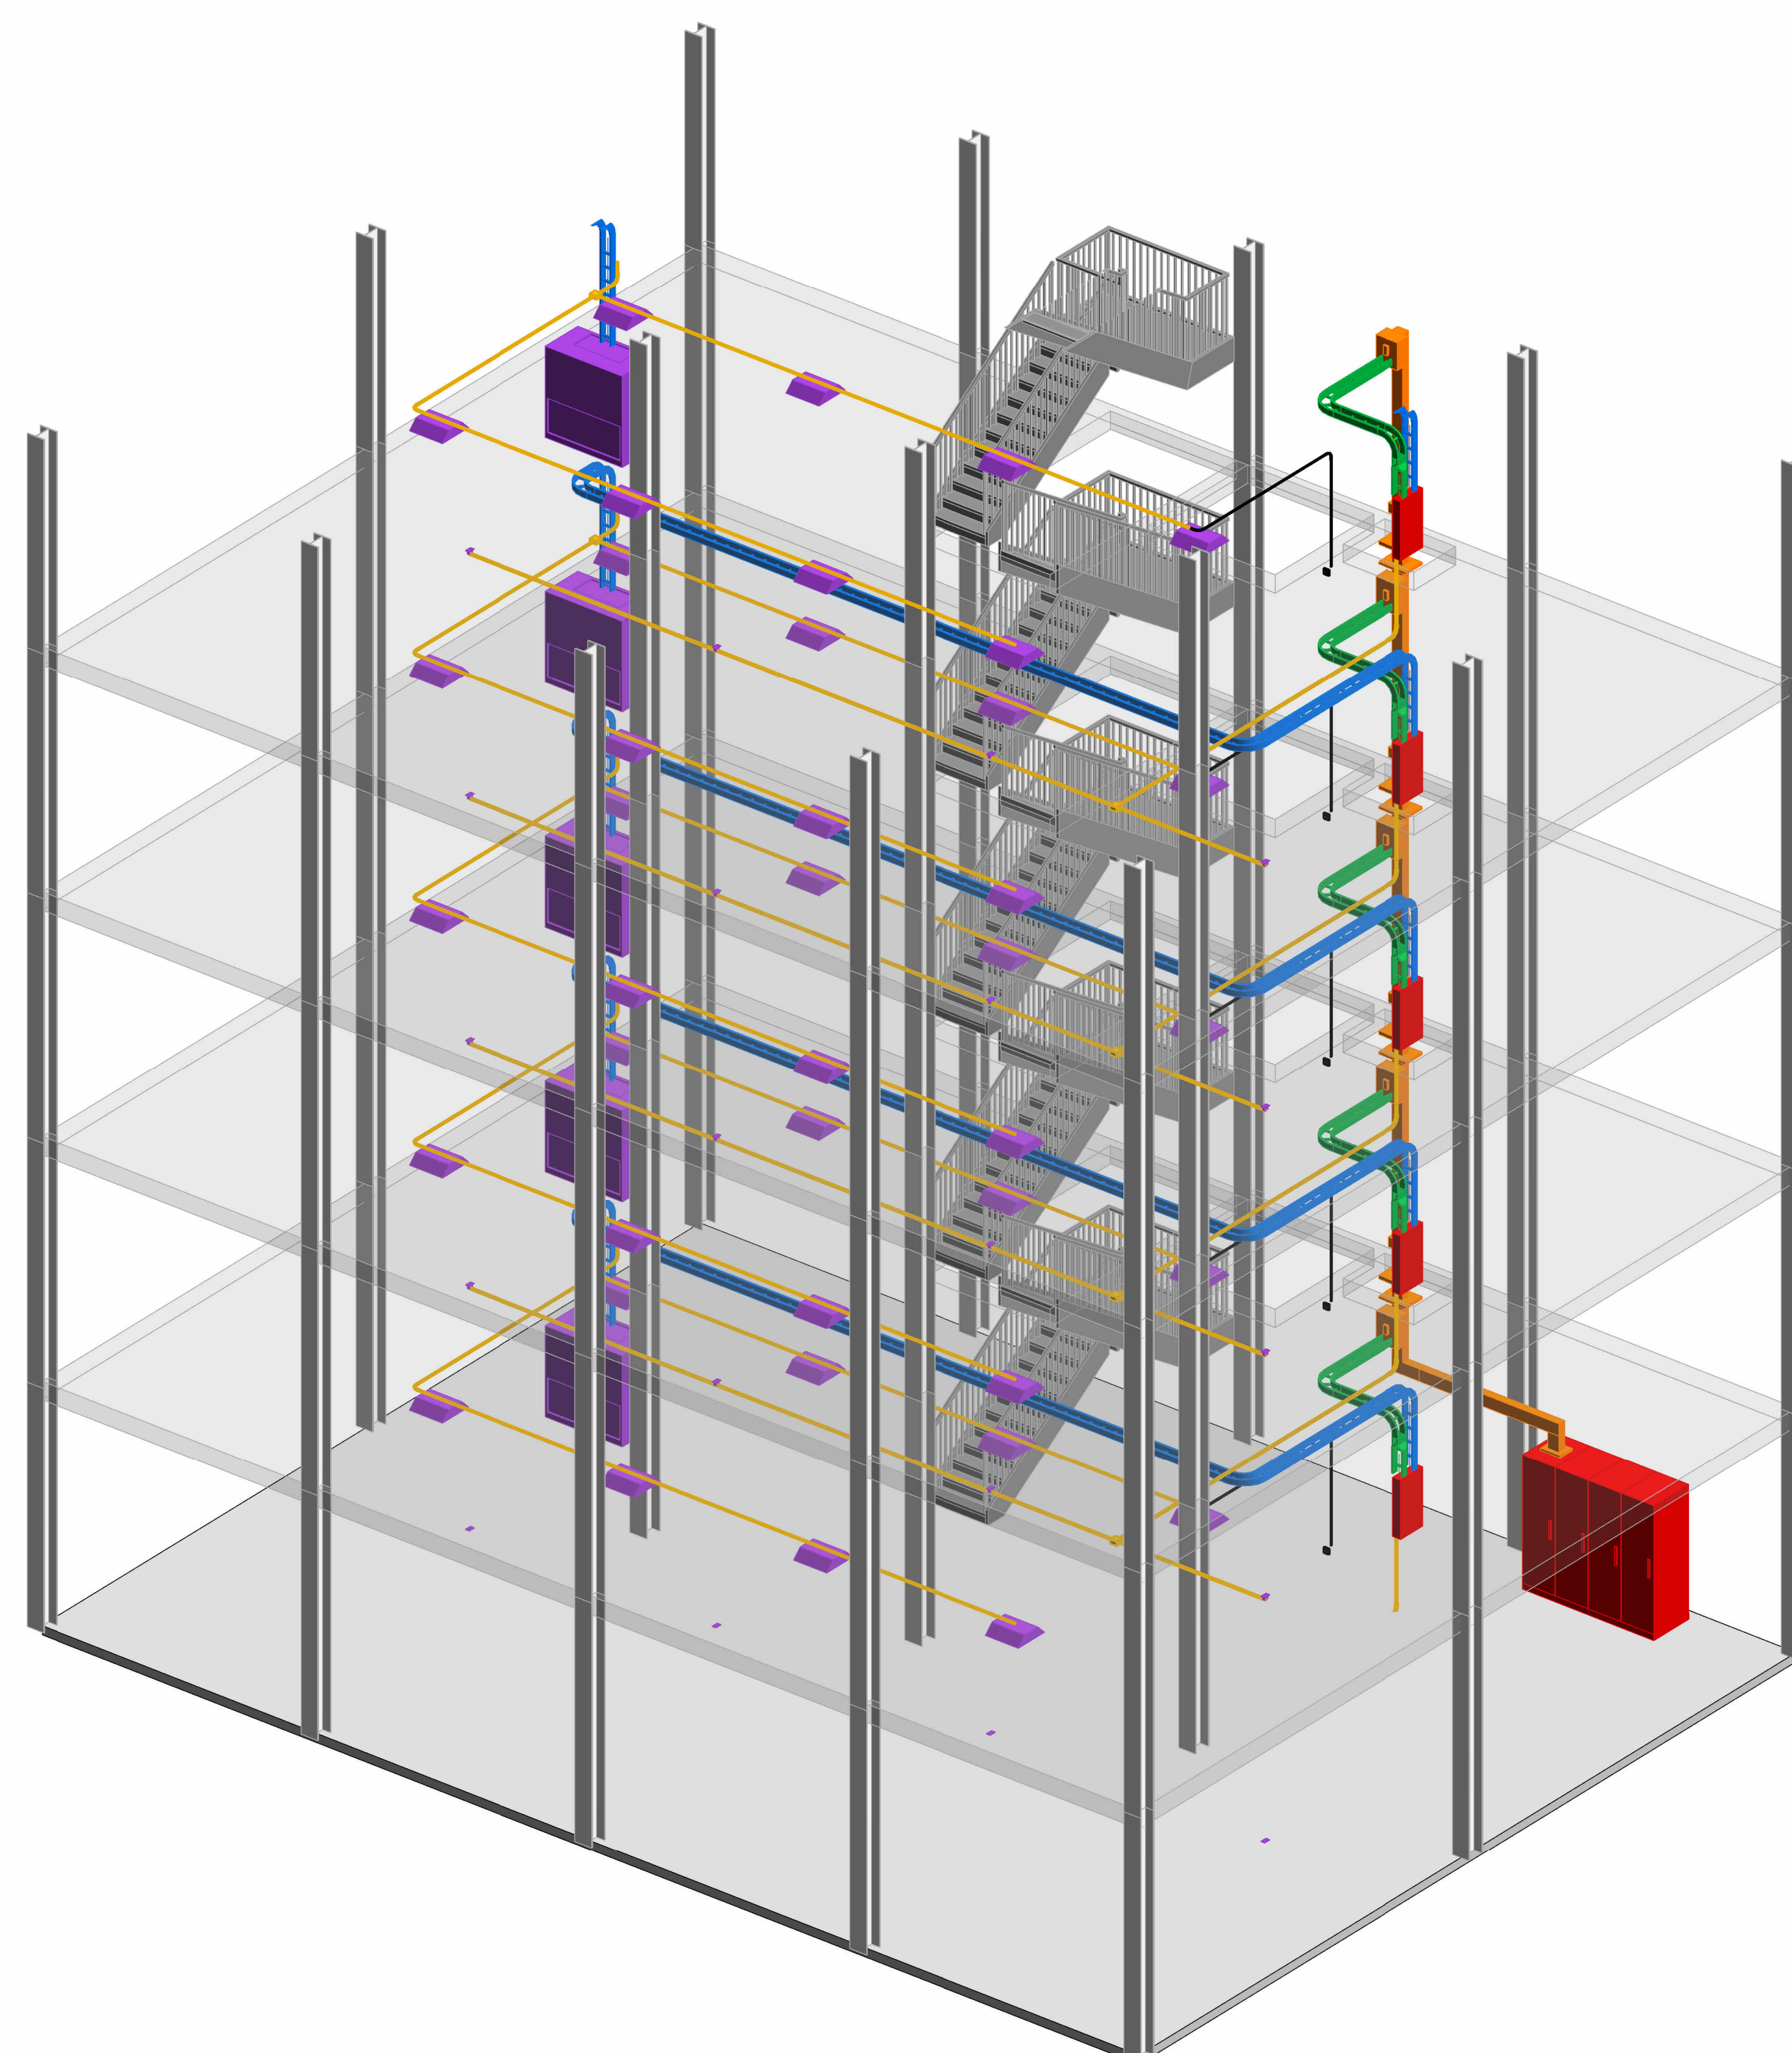

1 3D - Busduct System

[illegible]

**Latihan BIM
Gedung 5 Lantai -
Busduct**

Sistem Busduct - 3D Isometric

Project number	GB-BD-002
----------------	-----------

Date	25-09-2026
------	------------

Muhammad Sabiq Almuttaqin

Checked by	Checker
------------	---------

E-001

Scale

[illegible]

**Latihan BIM
Gedung 5 Lantai -
Busduct**

Denah Lantai Dasar - Busduct & Power

Project number	GB-BD-002
----------------	-----------

Date	25-09-2026
------	------------

Muhammad Sabiq Almuttadin

Checked by	Checker
------------	---------

E-101

Scale	1 : 50
-------	--------



www.autodesk.com/revit

Consultant
Address
Address
Phone
Fax
e-mail

Consultant
Address
Address
Phone
Fax
e-mail

Consultant
Address
Address
Phone
Fax
e-mail

Consultant
Address
Address
Phone
Fax
e-mail

[illegible]

**Latihan BIM
Gedung 5 Lantai -
Busduct**

Denah Tipikal Lantai 2-5 - Busduct & Power

Project number	GB-BD-002
----------------	-----------


Date	25-09-2026
------	------------

Muhammad Sabiq Almuttaqin

Checked by	Checker
------------	---------

E-102

Scale 1 : 50

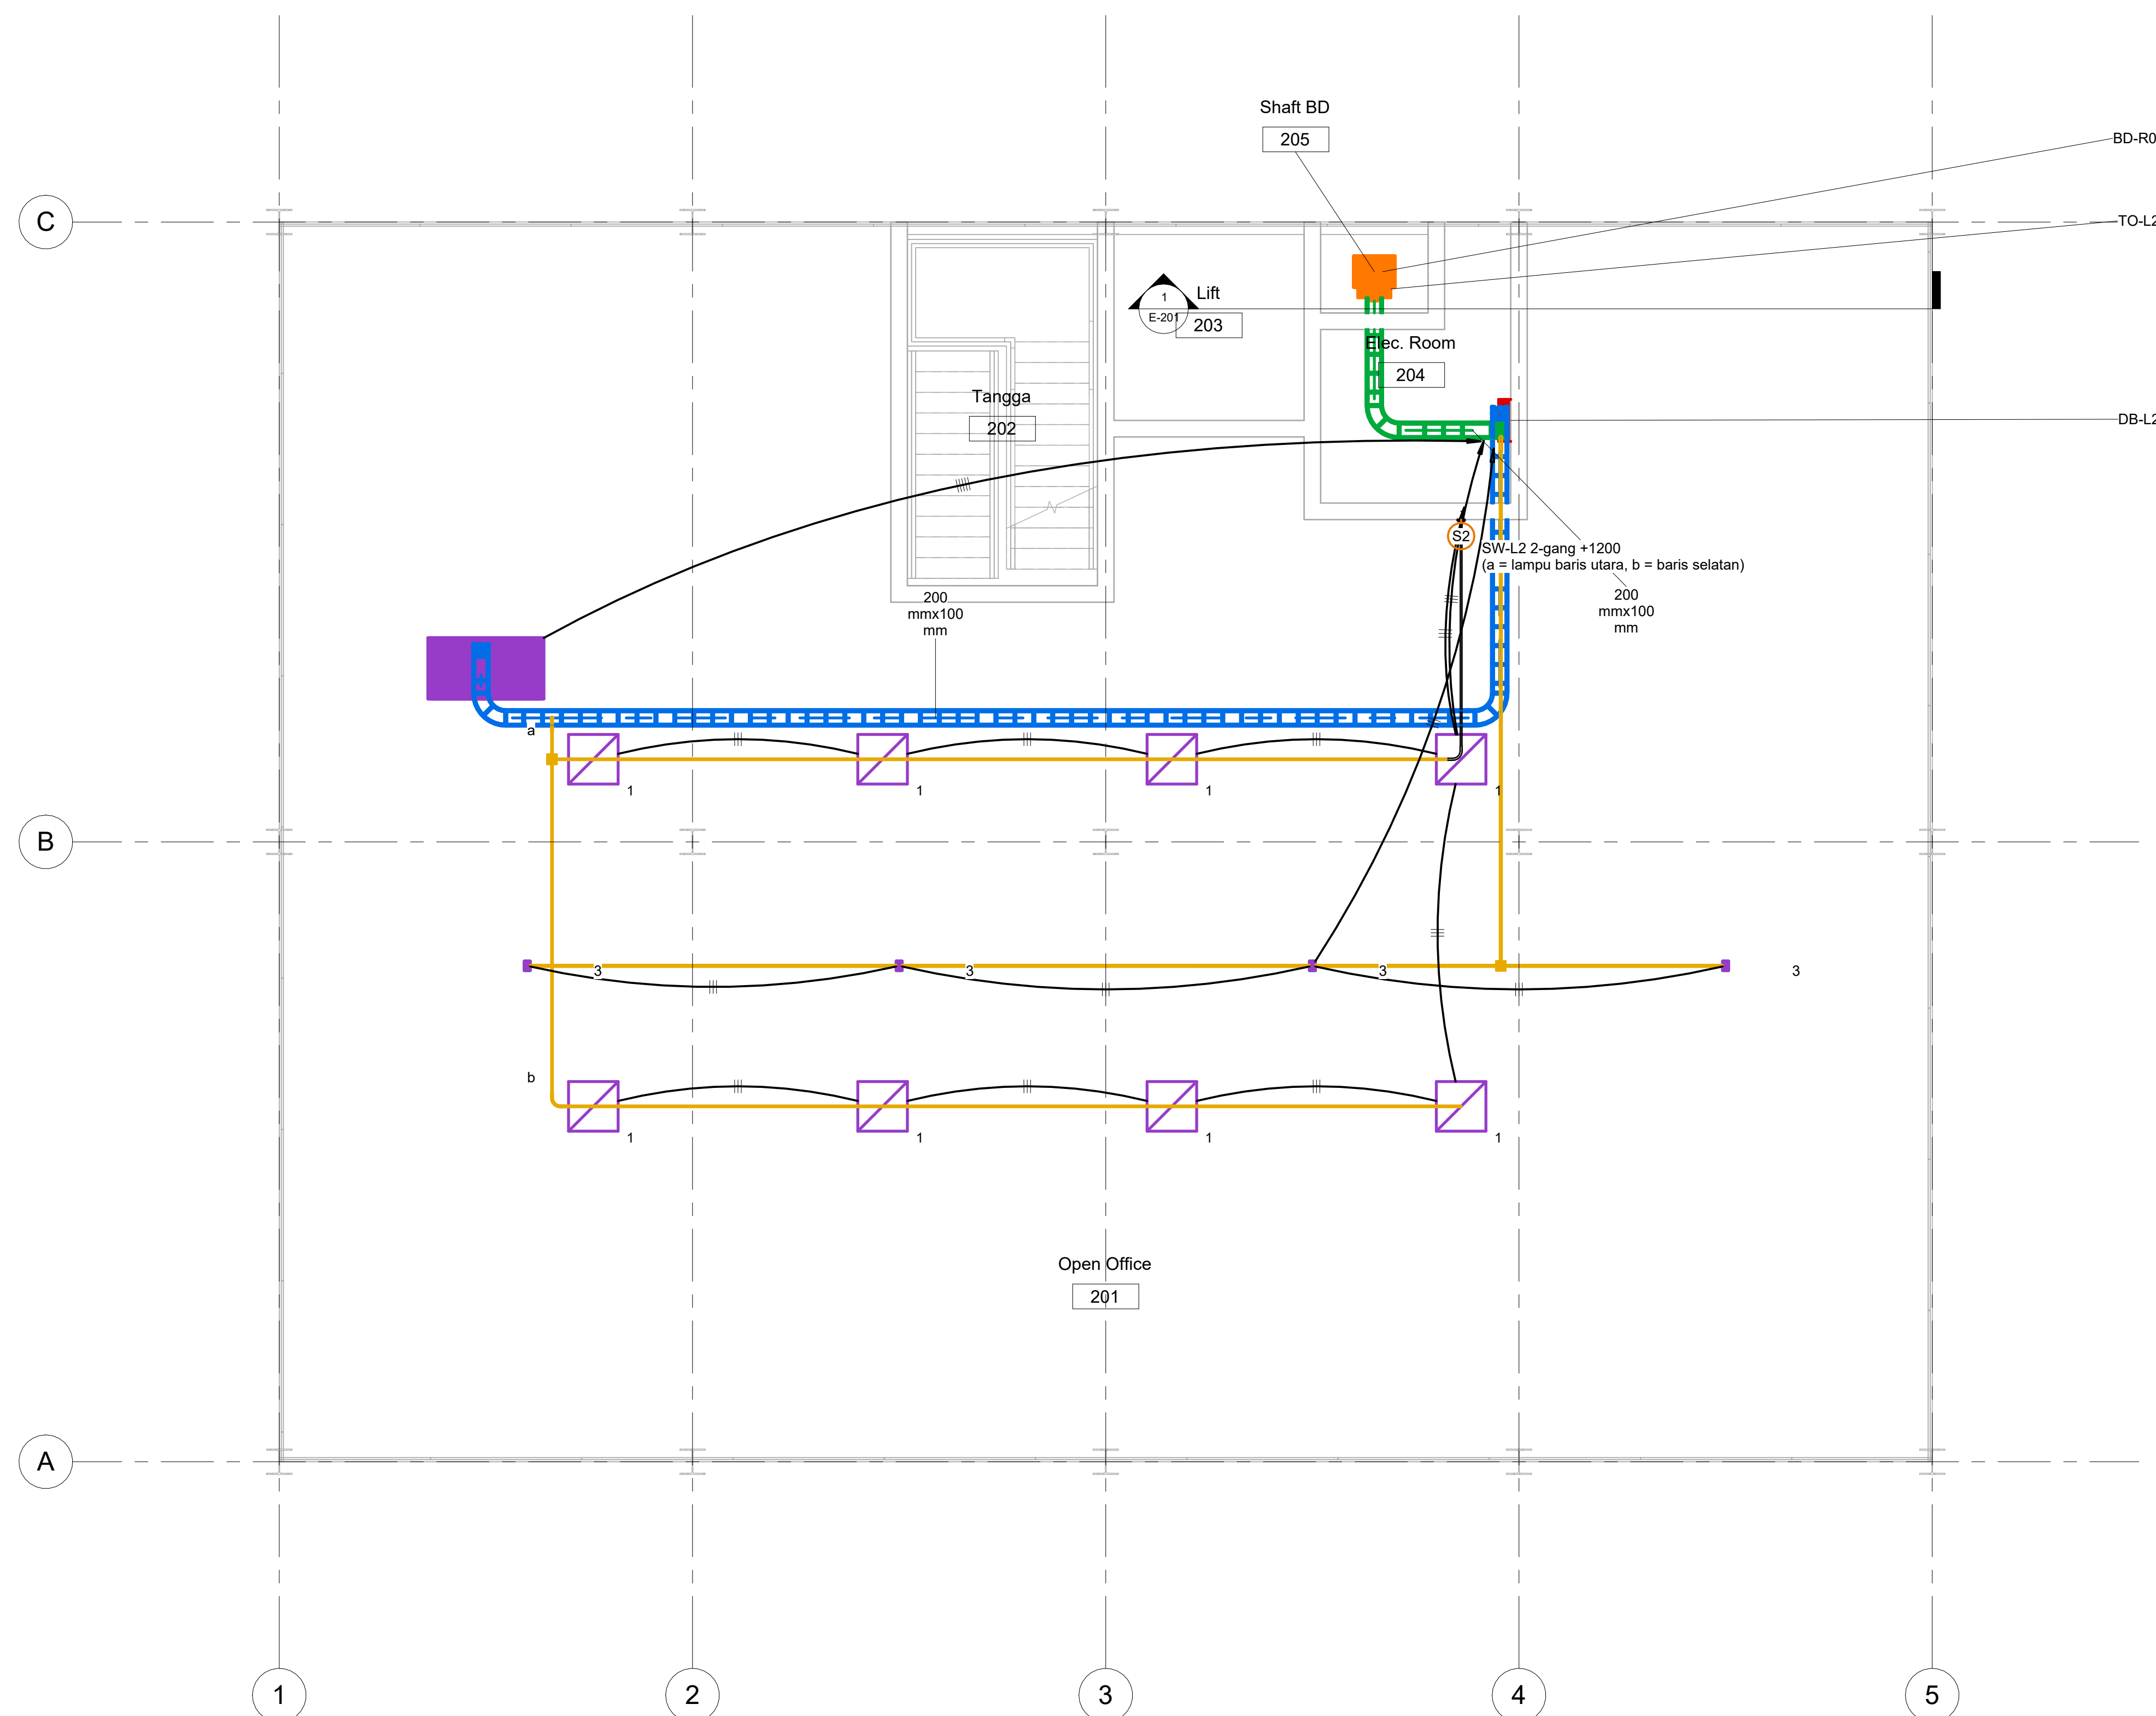

1 E-L2 Denah Tipikal Lantai
2-5 - Busduct & Power
1 : 50



www.autodesk.com/revit

Consultant
Address
Address
Phone
Fax
e-mail

Consultant
Address
Address
Phone
Fax
e-mail

Consultant
Address
Address
Phone
Fax
e-mail

Consultant
Address
Address
Phone
Fax
e-mail



SEC-01 Potongan Vertikal
1 Shaft Busduct
1:75

[illegible]

**Latihan BIM
Gedung 5 Lantai -
Busduct**

Potongan Vertikal Shaft Busduct (Riser)

Project number	GB-BD-002
----------------	-----------

Date	25-09-2026
------	------------

Muhammad Sabiq Almuttaqin

Checked by	Checker
------------	---------

E-201

Scale 1 : 75

Electrical Distribution Schedule								
Component Name	Type	Floor	Rating	Busduct Rating	Voltage	Phase	Connected Panel	System
CT-B-L1	Branch Cable Tray (DB-L1 to Loads)	Lantai 1	Branch circuits		230V / 400V	1P & 3P	DB-L1	Branch Cable Tray
CT-F-L1	Feeder Cable Tray (TO-L1 to DB-L1)	Lantai 1	NY Y 4x120mm2 + BC 70mm2		400/230V	3P+N+PE (4P)	TO-L1 / DB-L1	Feeder Cable Tray
CD-LT-L1	Lighting Conduit EMT 20mm	Lantai 1	NYM 3x2.5mm2 lighting circuit (contoh)		230V	1P+N+PE	DB-L1	Final Circuit Conduit
CD-SO-L1	Socket Conduit RNC 25mm (cast-in slab)	Lantai 1	NYM 3x4mm2 socket circuit (contoh)		230V	1P+N+PE	DB-L1	Final Circuit Conduit
BD-EL01	Busduct Elbow 90	Lantai 1	800A	800A	400/230V	3P+N+PE (4P)	LVMDP	LV Busduct Distribution
BD-FE	Busduct Flanged End	Lantai 1	800A	800A	400/230V	3P+N+PE (4P)	LVMDP	LV Busduct Distribution
BD-H01	Busduct Horizontal Feeder Section	Lantai 1	800A	800A	400/230V	3P+N+PE (4P)	LVMDP	LV Busduct Distribution
BD-R01	Vertical Busduct Riser Section	Lantai 1	800A	800A	400/230V	3P+N+PE (4P)	LVMDP	LV Busduct Distribution
TO-L1	Busduct Tap-Off Unit	Lantai 1	MCCB 250A 4P	800A	400/230V	3P+N+PE (4P)	DB-L1	LV Busduct Distribution
LVMDP	Main Switchboard	Lantai 1	1250A ACB 4P		400/230V	3P+N+PE (4P)	Trafo 1000 kVA (PLN)	LV Main Distribution
DB-L1	Sub Distribution Board (DB)	Lantai 1	250A MCCB 4P - 96 kVA		400/230V	3P+N+PE (4P)	LVMDP	Sub Distribution
CT-B-L2	Branch Cable Tray (DB-L2 to Loads)	Lantai 2	Branch circuits		230V / 400V	1P & 3P	DB-L2	Branch Cable Tray
CT-F-L2	Feeder Cable Tray (TO-L2 to DB-L2)	Lantai 2	NY Y 4x120mm2 + BC 70mm2		400/230V	3P+N+PE (4P)	TO-L2 / DB-L2	Feeder Cable Tray
CD-LT-L2	Lighting Conduit EMT 20mm	Lantai 2	NYM 3x2.5mm2 lighting circuit (contoh)		230V	1P+N+PE	DB-L2	Final Circuit Conduit
CD-SO-L2	Socket Conduit RNC 25mm (cast-in slab)	Lantai 2	NYM 3x4mm2 socket circuit (contoh)		230V	1P+N+PE	DB-L2	Final Circuit Conduit
BD-FB02	Busduct Floor Support & Fire Barrier	Lantai 2	800A	800A	400/230V	3P+N+PE (4P)	LVMDP	LV Busduct Distribution
BD-JP02	Busduct Joint Pack	Lantai 2	800A	800A	400/230V	3P+N+PE (4P)	LVMDP	LV Busduct Distribution
BD-R02	Vertical Busduct Riser Section	Lantai 2	800A	800A	400/230V	3P+N+PE (4P)	LVMDP	LV Busduct Distribution
TO-L2	Busduct Tap-Off Unit	Lantai 2	MCCB 250A 4P	800A	400/230V	3P+N+PE (4P)	DB-L2	LV Busduct Distribution
DB-L2	Sub Distribution Board (DB)	Lantai 2	250A MCCB 4P - 85 kVA		400/230V	3P+N+PE (4P)	LVMDP	Sub Distribution
CT-B-L3	Branch Cable Tray (DB-L3 to Loads)	Lantai 3	Branch circuits		230V / 400V	1P & 3P	DB-L3	Branch Cable Tray
CT-F-L3	Feeder Cable Tray (TO-L3 to DB-L3)	Lantai 3	NY Y 4x120mm2 + BC 70mm2		400/230V	3P+N+PE (4P)	TO-L3 / DB-L3	Feeder Cable Tray
CD-LT-L3	Lighting Conduit EMT 20mm	Lantai 3	NYM 3x2.5mm2 lighting circuit (contoh)		230V	1P+N+PE	DB-L3	Final Circuit Conduit
CD-SO-L3	Socket Conduit RNC 25mm (cast-in slab)	Lantai 3	NYM 3x4mm2 socket circuit (contoh)		230V	1P+N+PE	DB-L3	Final Circuit Conduit

Electrical Distribution Schedule								
Component Name	Type	Floor	Rating	Busduct Rating	Voltage	Phase	Connected Panel	System
BD-FB03	Busduct Floor Support & Fire Barrier	Lantai 3	800A	800A	400/230V	3P+N+PE (4P)	LVMDP	LV Busduct Distribution
BD-JP03	Busduct Joint Pack	Lantai 3	800A	800A	400/230V	3P+N+PE (4P)	LVMDP	LV Busduct Distribution
BD-R03	Vertical Busduct Riser Section	Lantai 3	800A	800A	400/230V	3P+N+PE (4P)	LVMDP	LV Busduct Distribution
TO-L3	Busduct Tap-Off Unit	Lantai 3	MCCB 250A 4P	800A	400/230V	3P+N+PE (4P)	DB-L3	LV Busduct Distribution
DB-L3	Sub Distribution Board (DB)	Lantai 3	250A MCCB 4P - 85 kVA		400/230V	3P+N+PE (4P)	LVMDP	Sub Distribution
CT-B-L4	Branch Cable Tray (DB-L4 to Loads)	Lantai 4	Branch circuits		230V / 400V	1P & 3P	DB-L4	Branch Cable Tray
CT-F-L4	Feeder Cable Tray (TO-L4 to DB-L4)	Lantai 4	NY Y 4x120mm2 + BC 70mm2		400/230V	3P+N+PE (4P)	TO-L4 / DB-L4	Feeder Cable Tray
CD-LT-L4	Lighting Conduit EMT 20mm	Lantai 4	NYM 3x2.5mm2 lighting circuit (contoh)		230V	1P+N+PE	DB-L4	Final Circuit Conduit
CD-SO-L4	Socket Conduit RNC 25mm (cast-in slab)	Lantai 4	NYM 3x4mm2 socket circuit (contoh)		230V	1P+N+PE	DB-L4	Final Circuit Conduit
BD-FB04	Busduct Floor Support & Fire Barrier	Lantai 4	800A	800A	400/230V	3P+N+PE (4P)	LVMDP	LV Busduct Distribution
BD-JP04	Busduct Joint Pack	Lantai 4	800A	800A	400/230V	3P+N+PE (4P)	LVMDP	LV Busduct Distribution
BD-R04	Vertical Busduct Riser Section	Lantai 4	800A	800A	400/230V	3P+N+PE (4P)	LVMDP	LV Busduct Distribution
TO-L4	Busduct Tap-Off Unit	Lantai 4	MCCB 250A 4P	800A	400/230V	3P+N+PE (4P)	DB-L4	LV Busduct Distribution
DB-L4	Sub Distribution Board (DB)	Lantai 4	250A MCCB 4P - 85 kVA		400/230V	3P+N+PE (4P)	LVMDP	Sub Distribution
CT-B-L5	Branch Cable Tray (DB-L5 to Loads)	Lantai 5	Branch circuits		230V / 400V	1P & 3P	DB-L5	Branch Cable Tray
CT-F-L5	Feeder Cable Tray (TO-L5 to DB-L5)	Lantai 5	NY Y 4x120mm2 + BC 70mm2		400/230V	3P+N+PE (4P)	TO-L5 / DB-L5	Feeder Cable Tray
CD-LT-L5	Lighting Conduit EMT 20mm	Lantai 5	NYM 3x2.5mm2 lighting circuit (contoh)		230V	1P+N+PE	DB-L5	Final Circuit Conduit
CD-SO-L5	Socket Conduit RNC 25mm (cast-in slab)	Lantai 5	NYM 3x4mm2 socket circuit (contoh)		230V	1P+N+PE	DB-L5	Final Circuit Conduit
BD-EC	Busduct End Cap	Lantai 5	800A	800A	400/230V	3P+N+PE (4P)	LVMDP	LV Busduct Distribution
BD-FB05	Busduct Floor Support & Fire Barrier	Lantai 5	800A	800A	400/230V	3P+N+PE (4P)	LVMDP	LV Busduct Distribution
BD-JP05	Busduct Joint Pack	Lantai 5	800A	800A	400/230V	3P+N+PE (4P)	LVMDP	LV Busduct Distribution
BD-R05	Vertical Busduct Riser Section	Lantai 5	800A	800A	400/230V	3P+N+PE (4P)	LVMDP	LV Busduct Distribution
TO-L5	Busduct Tap-Off Unit	Lantai 5	MCCB 250A 4P	800A	400/230V	3P+N+PE (4P)	DB-L5	LV Busduct Distribution
DB-L5	Sub Distribution Board (DB)	Lantai 5	250A MCCB 4P - 85 kVA		400/230V	3P+N+PE (4P)	LVMDP	Sub Distribution



www.autodesk.com/revit

Consultant
Address
Address
Phone
Fax
e-mail

Consultant
Address
Address
Phone
Fax
e-mail

Consultant
Address
Address
Phone
Fax
e-mail

Consultant
Address
Address
Phone
Fax
e-mail

[illegible]

Latihan BIM Gedung 5 Lantai - Busduct

Electrical Distribution Schedule

Project number GB-BD-002

Date 25-09-2026

Muhammad Sabiq Almuttadin

Checked by _____ Checker _____

E-202

Scale

Electrical Load Schedule							
Component Name	Type	Floor	Rating	Voltage	Phase	Connected Panel	System
AHU-L1	HVAC / Mechanical Load	Lantai 1	11 kW	400V	3P+N+PE	DB-L1	HVAC
CD-LT-L1	Lighting Conduit EMT 20mm	Lantai 1	NYM 3x2.5mm2 lighting circuit (contoh)	230V	1P+N+PE	DB-L1	Final Circuit Conduit
CD-LT-L1	Lighting Conduit EMT 20mm	Lantai 1	NYM 3x2.5mm2 lighting circuit (contoh)	230V	1P+N+PE	DB-L1	Final Circuit Conduit
CD-LT-L1	Lighting Conduit EMT 20mm	Lantai 1	NYM 3x2.5mm2 lighting circuit (contoh)	230V	1P+N+PE	DB-L1	Final Circuit Conduit
CD-LT-L1	Lighting Conduit EMT 20mm	Lantai 1	NYM 3x2.5mm2 lighting circuit (contoh)	230V	1P+N+PE	DB-L1	Final Circuit Conduit
CD-LT-L1	Lighting Conduit EMT 20mm	Lantai 1	NYM 3x2.5mm2 lighting circuit (contoh)	230V	1P+N+PE	DB-L1	Final Circuit Conduit
CD-LT-L1	Lighting Conduit EMT 20mm	Lantai 1	NYM 3x2.5mm2 lighting circuit (contoh)	230V	1P+N+PE	DB-L1	Final Circuit Conduit
CD-LT-L1	Lighting Conduit EMT 20mm	Lantai 1	NYM 3x2.5mm2 lighting circuit (contoh)	230V	1P+N+PE	DB-L1	Final Circuit Conduit
CD-LT-L1	Lighting Conduit EMT 20mm	Lantai 1	NYM 3x2.5mm2 lighting circuit (contoh)	230V	1P+N+PE	DB-L1	Final Circuit Conduit
CD-SO-L1	Socket Conduit RNC 25mm (cast-in slab)	Lantai 1	NYM 3x4mm2 socket circuit (contoh)	230V	1P+N+PE	DB-L1	Final Circuit Conduit
CD-SO-L1	Socket Conduit RNC 25mm (cast-in slab)	Lantai 1	NYM 3x4mm2 socket circuit (contoh)	230V	1P+N+PE	DB-L1	Final Circuit Conduit
CD-SO-L1	Socket Conduit RNC 25mm (cast-in slab)	Lantai 1	NYM 3x4mm2 socket circuit (contoh)	230V	1P+N+PE	DB-L1	Final Circuit Conduit
CD-SO-L1	Socket Conduit RNC 25mm (cast-in slab)	Lantai 1	NYM 3x4mm2 socket circuit (contoh)	230V	1P+N+PE	DB-L1	Final Circuit Conduit

Electrical Load Schedule							
Component Name	Type	Floor	Rating	Voltage	Phase	Connected Panel	System
CD-SO-L1	Socket Conduit RNC 25mm (cast-in slab)	Lantai 1	NYM 3x4mm2 socket circuit (contoh)	230V	1P+N+PE	DB-L1	Final Circuit Conduit
CD-SO-L1	Socket Conduit RNC 25mm (cast-in slab)	Lantai 1	NYM 3x4mm2 socket circuit (contoh)	230V	1P+N+PE	DB-L1	Final Circuit Conduit
LT-L1-01	Lighting Load (LED Panel)	Lantai 1	40 W	230V	1P+N+PE	DB-L1	Lighting
LT-L1-02	Lighting Load (LED Panel)	Lantai 1	40 W	230V	1P+N+PE	DB-L1	Lighting
LT-L1-03	Lighting Load (LED Panel)	Lantai 1	40 W	230V	1P+N+PE	DB-L1	Lighting
LT-L1-04	Lighting Load (LED Panel)	Lantai 1	40 W	230V	1P+N+PE	DB-L1	Lighting
LT-L1-05	Lighting Load (LED Panel)	Lantai 1	40 W	230V	1P+N+PE	DB-L1	Lighting
LT-L1-06	Lighting Load (LED Panel)	Lantai 1	40 W	230V	1P+N+PE	DB-L1	Lighting
LT-L1-07	Lighting Load (LED Panel)	Lantai 1	40 W	230V	1P+N+PE	DB-L1	Lighting
LT-L1-08	Lighting Load (LED Panel)	Lantai 1	40 W	230V	1P+N+PE	DB-L1	Lighting
SO-L1-01	Socket Outlet Load (Floor Box)	Lantai 1	16A / 1000 VA	230V	1P+N+PE	DB-L1	Power - Socket Outlet
SO-L1-02	Socket Outlet Load (Floor Box)	Lantai 1	16A / 1000 VA	230V	1P+N+PE	DB-L1	Power - Socket Outlet
SO-L1-03	Socket Outlet Load (Floor Box)	Lantai 1	16A / 1000 VA	230V	1P+N+PE	DB-L1	Power - Socket Outlet
SO-L1-04	Socket Outlet Load (Floor Box)	Lantai 1	16A / 1000 VA	230V	1P+N+PE	DB-L1	Power - Socket Outlet
AHU-L2	HVAC / Mechanical Load	Lantai 2	11 kW	400V	3P+N+PE	DB-L2	HVAC
CD-LT-L2	Lighting Conduit EMT 20mm	Lantai 2	NYM 3x2.5mm2 lighting circuit (contoh)	230V	1P+N+PE	DB-L2	Final Circuit Conduit
CD-LT-L2	Lighting Conduit EMT 20mm	Lantai 2	NYM 3x2.5mm2 lighting circuit (contoh)	230V	1P+N+PE	DB-L2	Final Circuit Conduit
CD-LT-L2	Lighting Conduit EMT 20mm	Lantai 2	NYM 3x2.5mm2 lighting circuit (contoh)	230V	1P+N+PE	DB-L2	Final Circuit Conduit
CD-LT-L2	Lighting Conduit EMT 20mm	Lantai 2	NYM 3x2.5mm2 lighting circuit (contoh)	230V	1P+N+PE	DB-L2	Final Circuit Conduit
CD-LT-L2	Lighting Conduit EMT 20mm	Lantai 2	NYM 3x2.5mm2 lighting circuit (contoh)	230V	1P+N+PE	DB-L2	Final Circuit Conduit
CD-LT-L2	Lighting Conduit EMT 20mm	Lantai 2	NYM 3x2.5mm2 lighting circuit (contoh)	230V	1P+N+PE	DB-L2	Final Circuit Conduit
CD-LT-L2	Lighting Conduit EMT 20mm	Lantai 2	NYM 3x2.5mm2 lighting circuit (contoh)	230V	1P+N+PE	DB-L2	Final Circuit Conduit
CD-LT-L2	Lighting Conduit EMT 20mm	Lantai 2	NYM 3x2.5mm2 lighting circuit (contoh)	230V	1P+N+PE	DB-L2	Final Circuit Conduit
CD-LT-L2	Lighting Conduit EMT 20mm	Lantai 2	NYM 3x2.5mm2 lighting circuit (contoh)	230V	1P+N+PE	DB-L2	Final Circuit Conduit
CD-SO-L2	Socket Conduit RNC 25mm (cast-in slab)	Lantai 2	NYM 3x4mm2 socket circuit (contoh)	230V	1P+N+PE	DB-L2	Final Circuit Conduit
CD-SO-L2	Socket Conduit RNC 25mm (cast-in slab)	Lantai 2	NYM 3x4mm2 socket circuit (contoh)	230V	1P+N+PE	DB-L2	Final Circuit Conduit
CD-SO-L2	Socket Conduit RNC 25mm (cast-in slab)	Lantai 2	NYM 3x4mm2 socket circuit (contoh)	230V	1P+N+PE	DB-L2	Final Circuit Conduit
CD-SO-L2	Socket Conduit RNC 25mm (cast-in slab)	Lantai 2	NYM 3x4mm2 socket circuit (contoh)	230V	1P+N+PE	DB-L2	Final Circuit Conduit
CD-SO-L2	Socket Conduit RNC 25mm (cast-in slab)	Lantai 2	NYM 3x4mm2 socket circuit (contoh)	230V	1P+N+PE	DB-L2	Final Circuit Conduit
CD-SO-L2	Socket Conduit RNC 25mm (cast-in slab)	Lantai 2	NYM 3x4mm2 socket circuit (contoh)	230V	1P+N+PE	DB-L2	Final Circuit Conduit
LT-L2-01	Lighting Load (LED Panel)	Lantai 2	40 W	230V	1P+N+PE	DB-L2	Lighting
LT-L2-02	Lighting Load (LED Panel)	Lantai 2	40 W	230V	1P+N+PE	DB-L2	Lighting
LT-L2-03	Lighting Load (LED Panel)	Lantai 2	40 W	230V	1P+N+PE	DB-L2	Lighting
LT-L2-04	Lighting Load (LED Panel)	Lantai 2	40 W	230V	1P+N+PE	DB-L2	Lighting
LT-L2-05	Lighting Load (LED Panel)	Lantai 2	40 W	230V	1P+N+PE	DB-L2	Lighting
LT-L2-06	Lighting Load (LED Panel)	Lantai 2	40 W	230V	1P+N+PE	DB-L2	Lighting
LT-L2-07	Lighting Load (LED Panel)	Lantai 2	40 W	230V	1P+N+PE	DB-L2	Lighting
LT-L2-08	Lighting Load (LED Panel)	Lantai 2	40 W	230V	1P+N+PE	DB-L2	Lighting
SO-L2-01	Socket Outlet Load (Floor Box)	Lantai 2	16A / 1000 VA	230V	1P+N+PE	DB-L2	Power - Socket Outlet
SO-L2-02	Socket Outlet Load (Floor Box)	Lantai 2	16A / 1000 VA	230V	1P+N+PE	DB-L2	Power - Socket Outlet
SO-L2-03	Socket Outlet Load (Floor Box)	Lantai 2	16A / 1000 VA	230V	1P+N+PE	DB-L2	Power - Socket Outlet
SO-L2-04	Socket Outlet Load (Floor Box)	Lantai 2	16A / 1000 VA	230V	1P+N+PE	DB-L2	Power - Socket Outlet
AHU-L3	HVAC / Mechanical Load	Lantai 3	11 kW	400V	3P+N+PE	DB-L3	HVAC
CD-LT-L3	Lighting Conduit EMT 20mm	Lantai 3	NYM 3x2.5mm2 lighting circuit (contoh)	230V	1P+N+PE	DB-L3	Final Circuit Conduit
CD-LT-L3	Lighting Conduit EMT 20mm	Lantai 3	NYM 3x2.5mm2 lighting circuit (contoh)	230V	1P+N+PE	DB-L3	Final Circuit Conduit



AUTODESK

www.autodesk.com/revit

Consultant	Consultant
Address	Address
Address	Address
Phone	Phone
Fax	Fax
e-mail	e-mail
Consultant	Consultant
Address	Address
Address	Address
Phone	Phone
Fax	Fax
e-mail	e-mail

[illegible]

Latihan BIM	
Gedung 5 Lantai - Busduct	
Electrical Load Schedule	
Project number	GB-BD-002
Date	25-09-2026
Muhammad Sabiq Almuttaqin	
Checked by	Checker
E-301	
Scale	

Branch Panel: DB-L1																			
Location: Elec. Room 104				Volts: 400/230V 3P4W 50Hz				A.I.C. Rating:											
Supply From: LVMDP				Phases: 3				Mains Type:											
Mounting: Recessed				Wires: 4				Mains Rating: 100 A											
Enclosure: Type 1				MCB Rating: 1 A															
Notes:																			
CKT	Circuit Description	Trip	Poles	A		B		C		Poles	Trip	Circuit Description	CKT						
1	Lighting - Open Office (SW-L1)	10 A	1	352 VA	4300...					3	25 A	AHU-L1 11 kW	2						
3	Floor Box Sockets	16 A	1			800 VA	4300...			--	--	--	4						
5								4300...		--	--	--	6						
7													8						
9													10						
11													12						
13													14						
15													16						
17													18						
19													20						
21													22						
23													24						
25													26						
27													28						
29													30						
31													32						
33													34						
35													36						
37													38						
39													40						
41													42						
Total Load:				4635 VA		4963 VA		4300 VA											
Total Amps:				20 A		22 A		19 A											
Legend:																			
Load Classification		Connected Load		Demand Factor		Estimated Demand		Panel Totals											
Cooling		12900 VA		100.00%		12900 VA													
Receptacle		800 VA		100.00%		800 VA		Total Conn. Load: 13886 VA											
Lighting		352 VA		100.00%		352 VA		Total Est. Demand: 13886 VA											
								Total Conn.: 20 A											
								Total Est. Demand: 20 A											

[illegible]

Branch Panel: DB-L2																			
Location: Elec. Room 204				Volts: 400/230V 3P4W 50Hz				A.I.C. Rating:											
Supply From: LVMDP				Phases: 3				Mains Type:											
Mounting: Recessed				Wires: 4				Mains Rating: 100 A											
Enclosure: Type 1				MCB Rating: 1 A															
Notes:																			
CKT	Circuit Description	Trip	Poles	A		B		C		Poles	Trip	Circuit Description	CKT						
1	Lighting - Open Office (SW-L2)	10 A	1	352 VA	4300...					3	25 A	AHU-L2 11 kW	2						
3	Floor Box Sockets	16 A	1			800 VA	4300...			--	--	--	4						
5								4300...		--	--	--	6						
7													8						
9													10						
11													12						
13													14						
15													16						
17													18						
19													20						
21													22						
23													24						
25													26						
27													28						
29													30						
31													32						
33													34						
35													36						
37													38						
39													40						
41													42						
Total Load:				4635 VA		4963 VA		4300 VA											
Total Amps:				20 A		22 A		19 A											
Legend:																			
Load Classification		Connected Load		Demand Factor		Estimated Demand		Panel Totals											
Cooling		12900 VA		100.00%		12900 VA													
Receptacle		800 VA		100.00%		800 VA		Total Conn. Load: 13886 VA											
Lighting		352 VA		100.00%		352 VA		Total Est. Demand: 13886 VA											
								Total Conn.: 20 A											
								Total Est. Demand: 20 A											

Branch Panel: DB-L4																			
Location: Elec. Room 404				Volts: 400/230V 3P4W 50Hz				A.I.C. Rating:											
Supply From: LVMDP				Phases: 3				Mains Type:											
Mounting: Recessed				Wires: 4				Mains Rating: 100 A											
Enclosure: Type 1				MCB Rating: 1 A															
Notes:																			
CKT	Circuit Description	Trip	Poles	A		B		C		Poles	Trip	Circuit Description	CKT						
1	Lighting - Open Office (SW-L4)	10 A	1	352 VA	4300...					3	25 A	AHU-L4 11 kW	2						
3	Floor Box Sockets	16 A	1			800 VA	4300...			--	--	--	4						
5								4300...		--	--	--	6						
7													8						
9													10						
11													12						
13													14						
15													16						
17													18						
19													20						
21													22						
23													24						
25													26						
27													28						
29													30						
31													32						
33													34						
35													36						
37													38						
39													40						
41													42						
Total Load:				4635 VA		4963 VA		4300 VA											
Total Amps:				20 A		22 A		19 A											
Legend:																			
Load Classification		Connected Load		Demand Factor		Estimated Demand		Panel Totals											
Cooling		12900 VA		100.00%		12900 VA													
Receptacle		800 VA		100.00%		800 VA		Total Conn. Load: 13886 VA											
Lighting		352 VA		100.00%		352 VA		Total Est. Demand: 13886 VA											
								Total Conn.: 20 A											
								Total Est. Demand: 20 A											



www.autodesk.com/revit

Consultant
Address
Address
Phone
Fax
e-mail

Consultant
Address
Address
Phone
Fax
e-mail

[illegible]

Latihan BIM Gedung 5 Lantai - Busduct

Panel Schedule DB-L1 - DB-L4

Project number GB-BD-002

Date 25-09-2026

Muhammad Sabiq Almuttaqin

Checked by _____ Checker _____

E-302

Scale

