




www.autodesk.com/revit

Consultant
Address
Address
Phone
Fax
e-mail

Consultant
Address
Address
Phone
Fax
e-mail

Consultant
Address
Address
Phone
Fax
e-mail


Consultant
Address
Address
Phone
Fax
e-mail

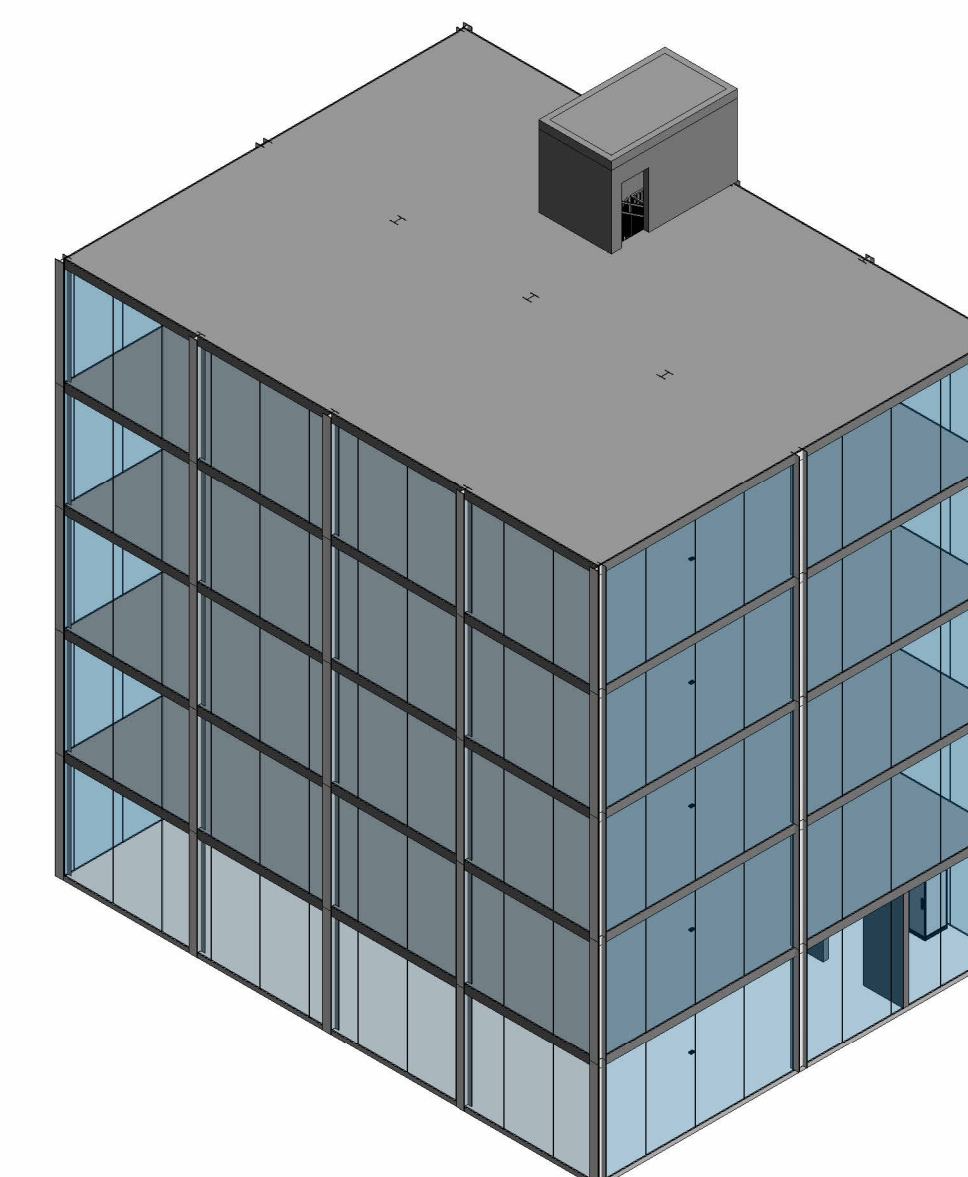

2 3D - Gedung 5 Lantai

LEGENDA SISTEM (GRAPHIC OVERRIDE)
 ORANYE : LV Busduct 800A Cu 4P+PE (3P+N+PE) 400/230V
 MERAH : LVMDP 1250A & DB-L1 s/d DB-L5 (250A)
 HIJAU : Feeder Cable Tray Tap-Off -> DB
 BIRU : Branch Cable Tray DB -> Beban
 UNGU : Beban (Lighting, Socket Outlet, AHU/HVAC)
 ABU-ABU (half tone) : Arsitektur & Struktur

ALUR DISTRIBUSI:
Trafo -> LVMDP -> Busduct Horizontal (BD-H01) -> Elbow ->
Vertical Busduct Riser (BD-R01..R05) -> Tap-Off (TO-Lx) ->
Feeder Tray -> DB-Lx -> Branch Tray -> Beban

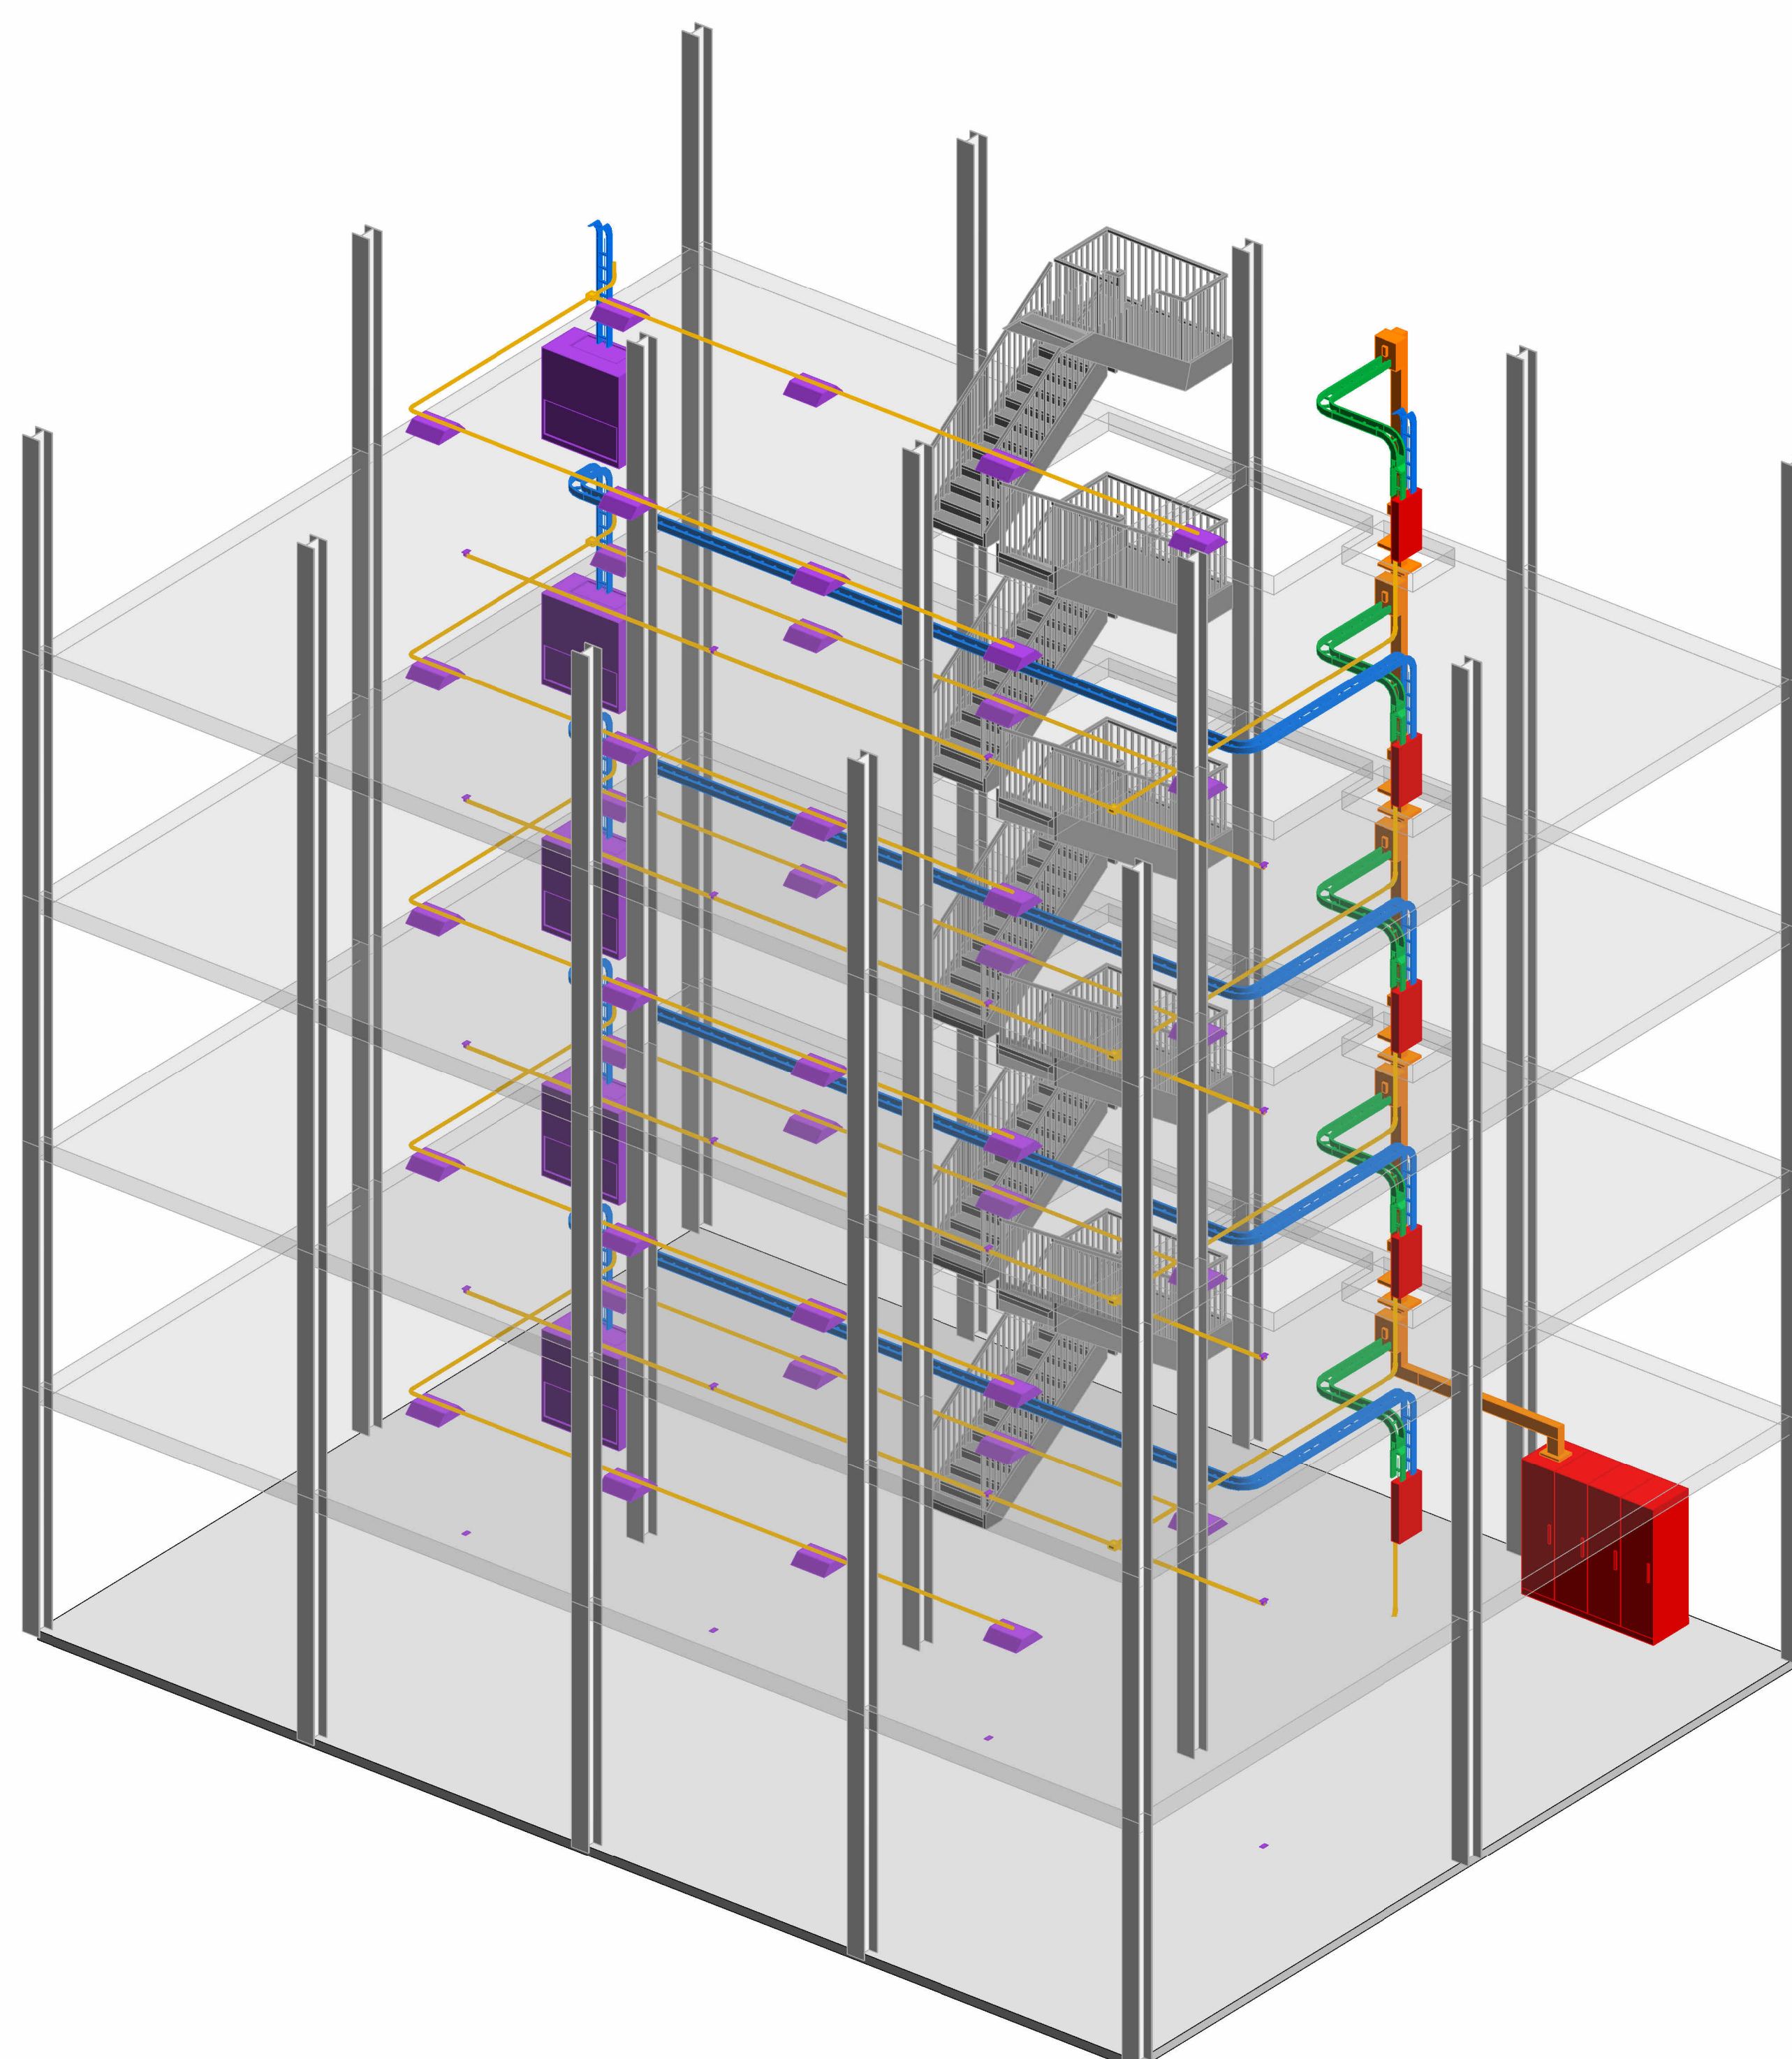

1 3D - Busduct System

[illegible]

**Latihan BIM
Gedung 5 Lantai -
Busduct**

Sistem Busduct - 3D Isometric

Project number	GB-BD-002
----------------	-----------

Date	25-09-2026
------	------------

Muhammad Sabiq Almuttaqin

Checked by	Checker
------------	---------

E-001

Scale




www.autodesk.com/revit

Consultant
Address
Address
Phone
Fax
e-mail

Consultant
Address
Address
Phone
Fax
e-mail

Consultant
Address
Address
Phone
Fax
e-mail

Consultant
Address
Address
Phone
Fax
e-mail

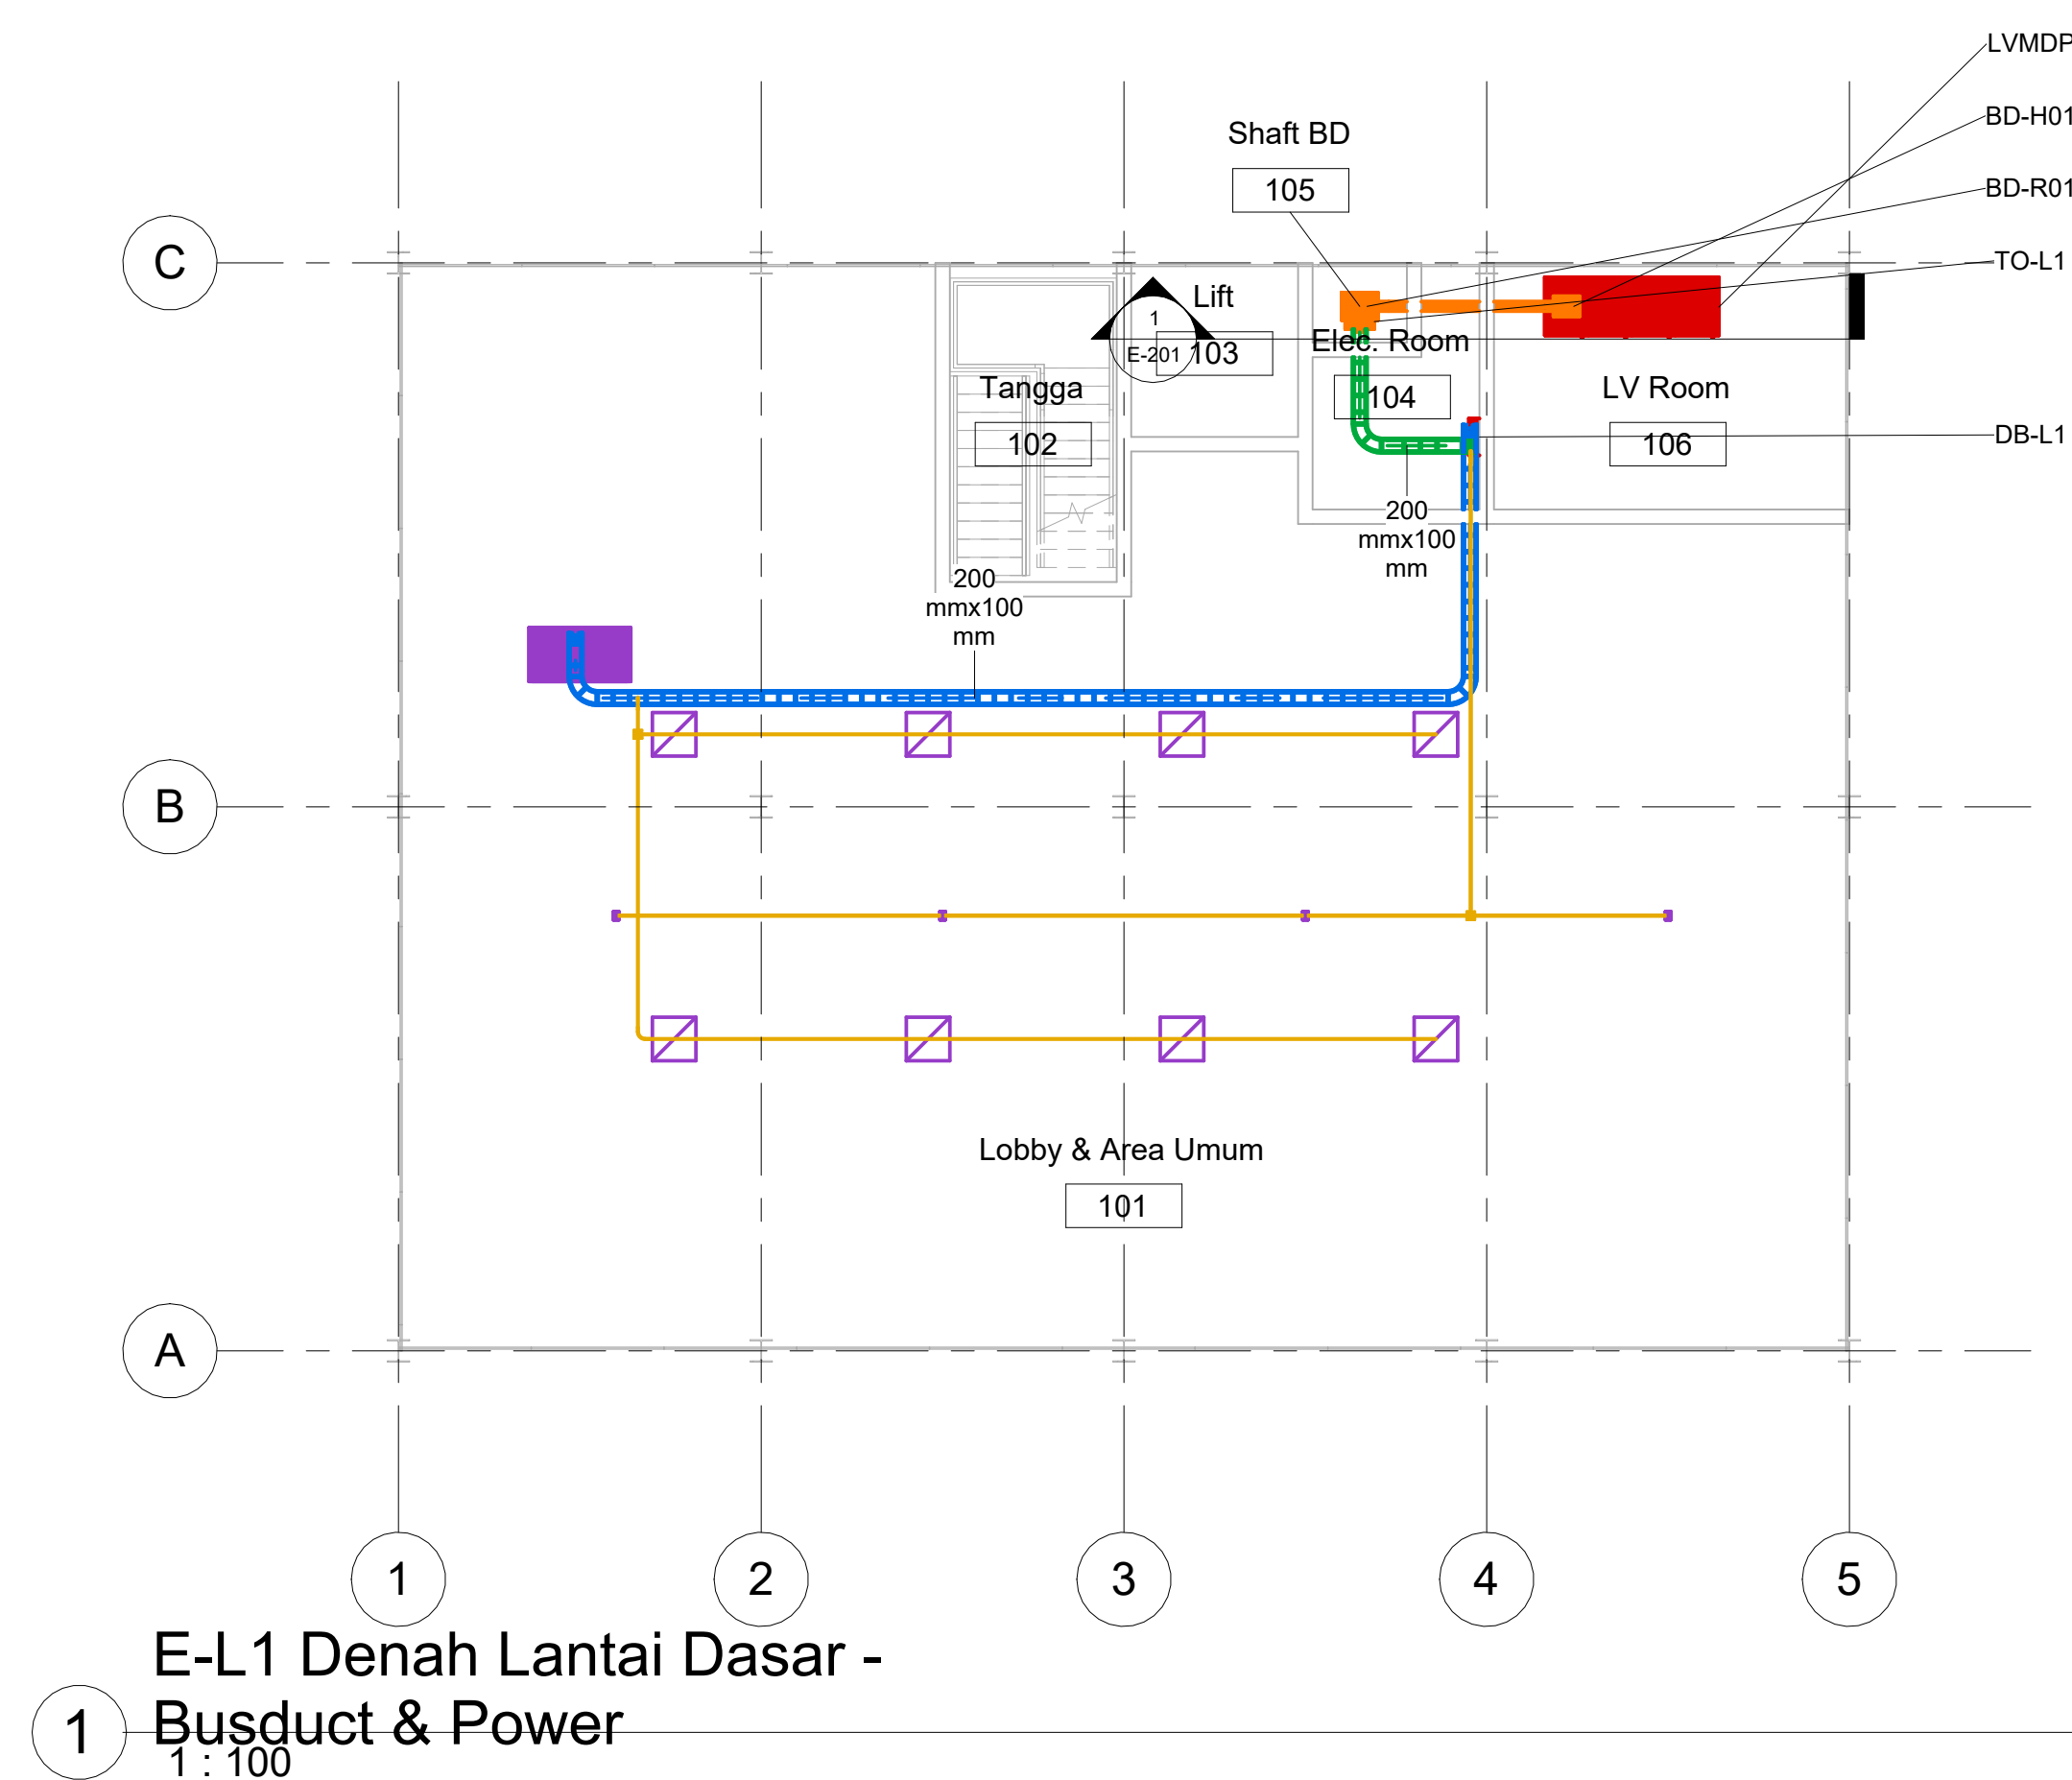[illegible]

**Latihan BIM
Gedung 5 Lantai -
Busduct**

Denah Lantai Dasar - Busduct & Power

Project number	GB-BD-002
----------------	-----------

Date	25-09-2026
------	------------

Muhammad Sabiq Almuttadin

Checked by	Checker
------------	---------

E-101

Scale	1 : 100
-------	---------




www.autodesk.com/revit

Consultant
Address
Address
Phone
Fax
e-mail

Consultant
Address
Address
Phone
Fax
e-mail

Consultant
Address
Address
Phone
Fax
e-mail

Consultant
Address
Address
Phone
Fax
e-mail

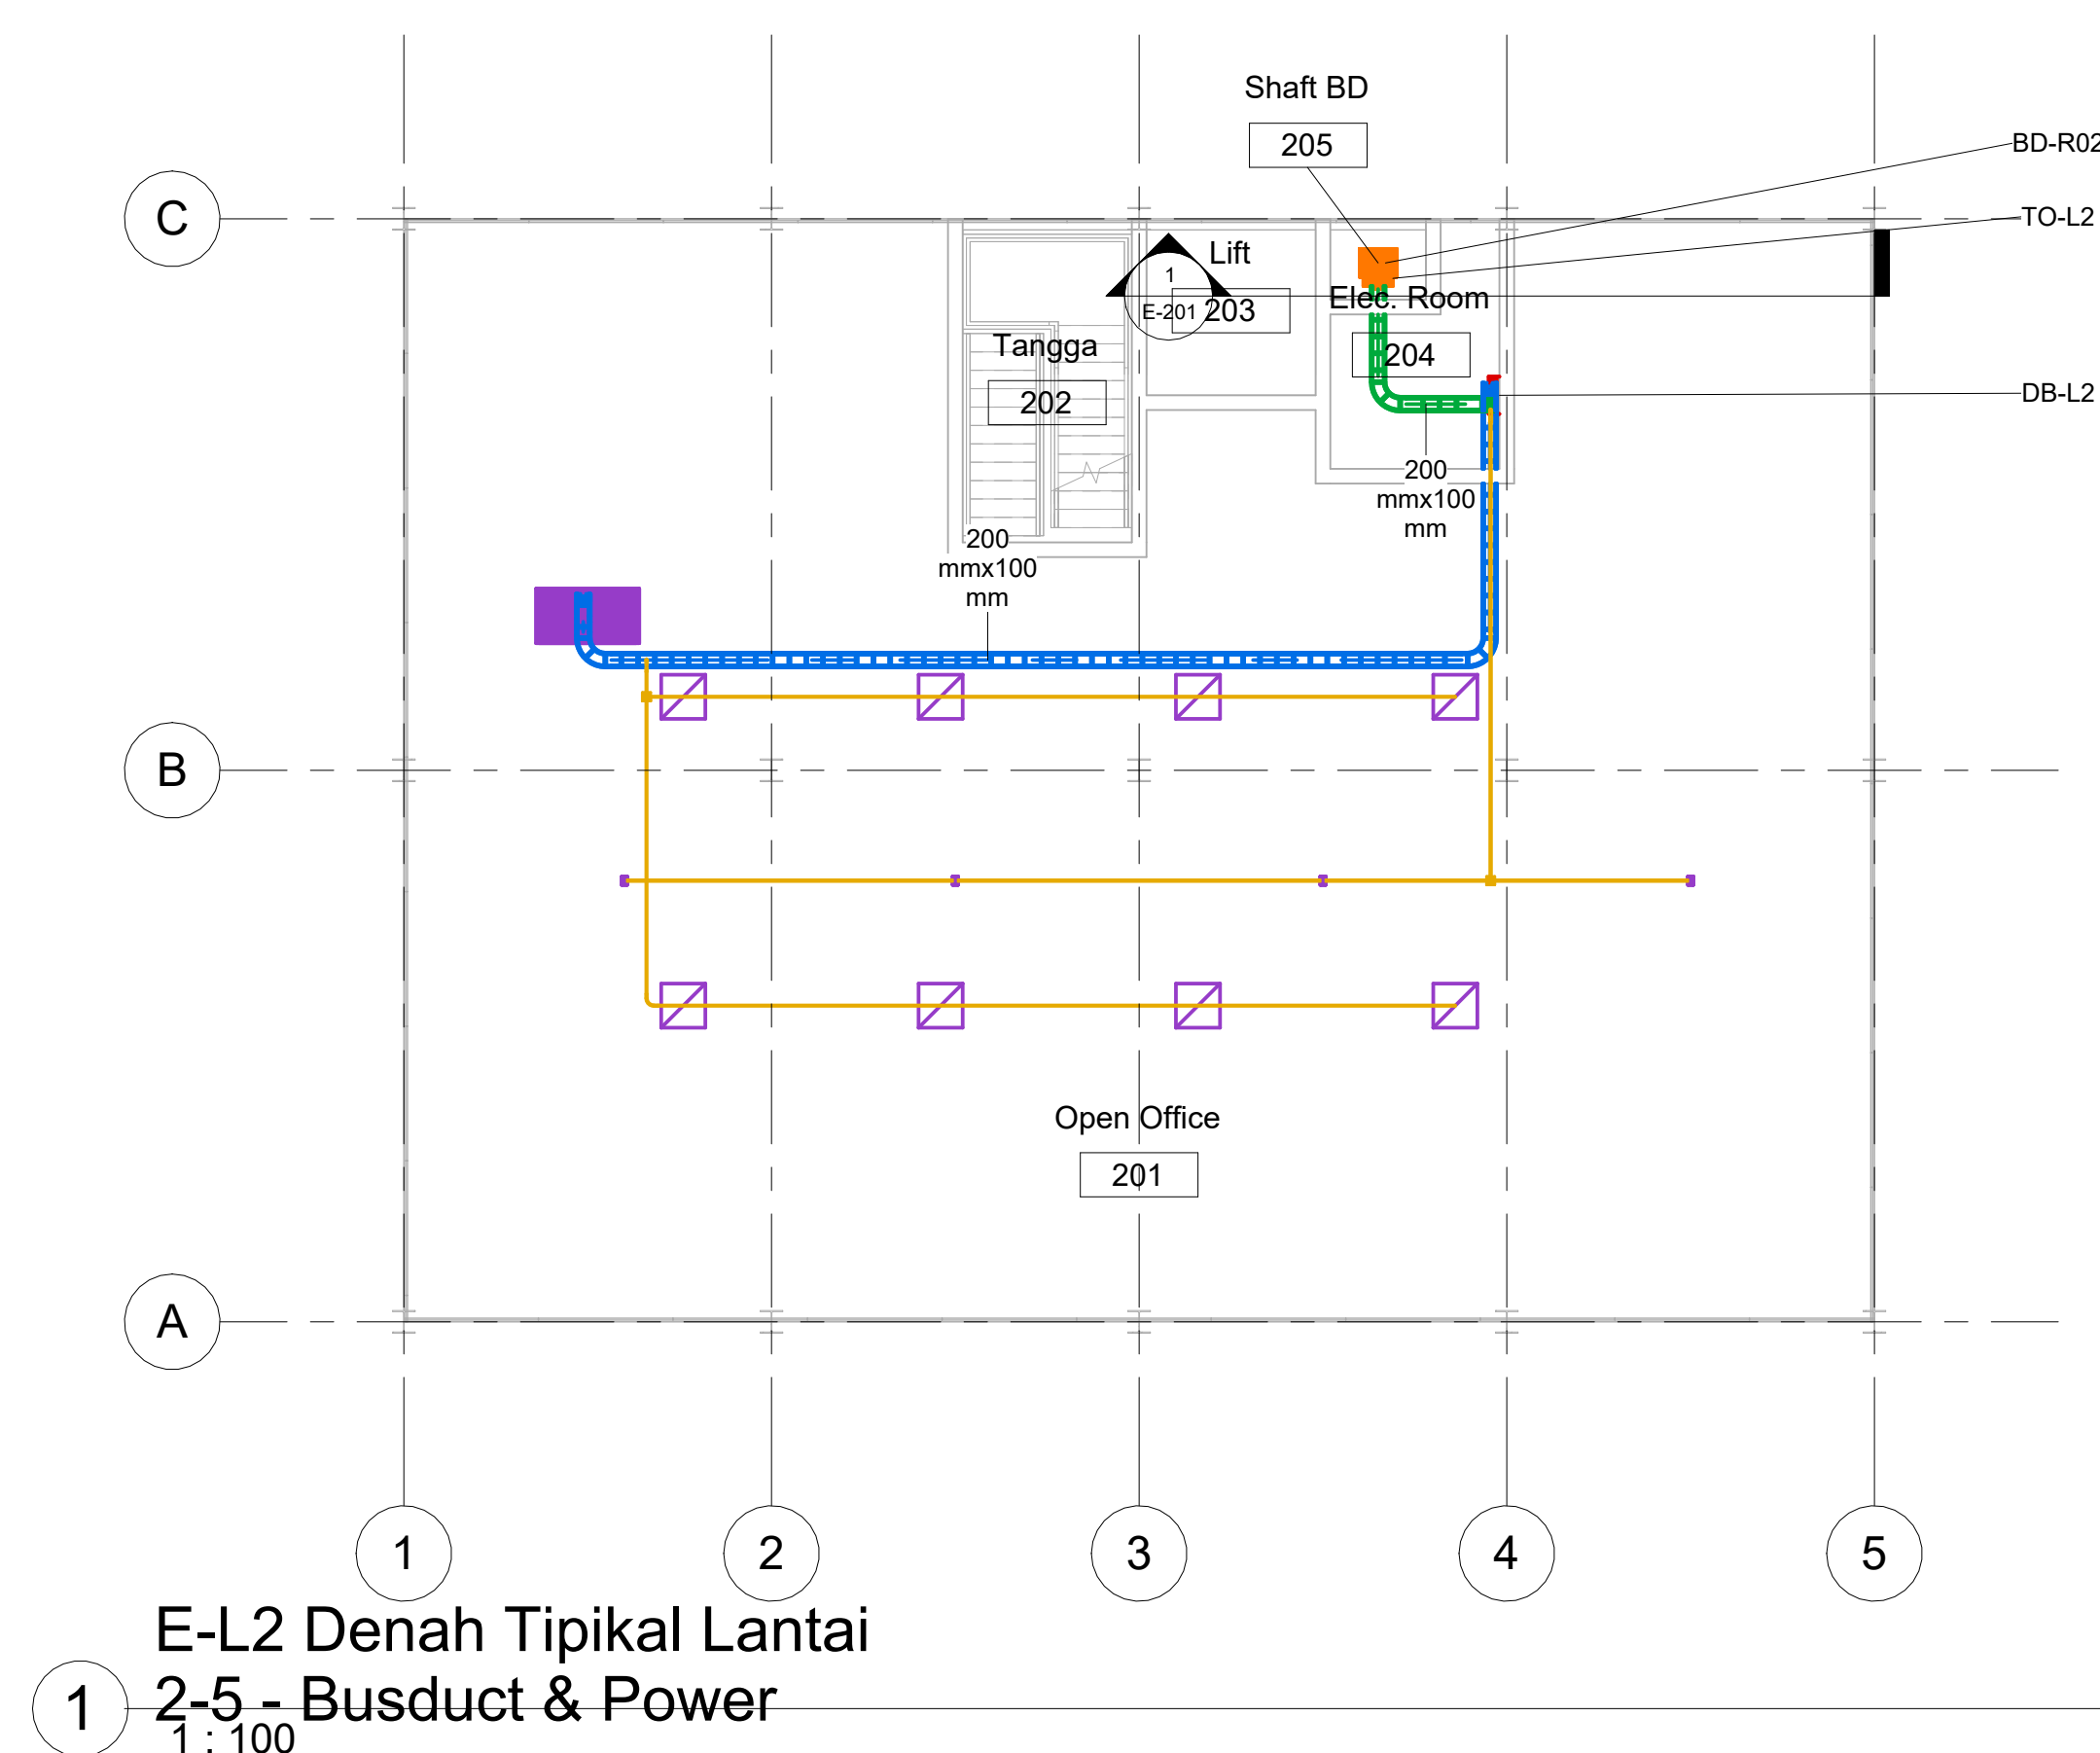[illegible]

**Latihan BIM
Gedung 5 Lantai -
Busduct**

Denah Tipikal Lantai 2-5 - Busduct & Power

Project number	GB-BD-002
Date	25-09-2026
Muhammad Sobiq Almuttaqin	
Checked by	Checker
E-102	
Scale	1 : 100



www.autodesk.com/revit

Consultant
Address
Address
Phone
Fax
e-mail

Consultant
Address
Address
Phone
Fax
e-mail

Consultant
Address
Address
Phone
Fax
e-mail

Consultant
Address
Address
Phone
Fax
e-mail



SEC-01 Potongan Vertikal
1 Shaft Busduct
1:75

[illegible]

**Latihan BIM
Gedung 5 Lantai -
Busduct**

Potongan Vertikal Shaft Busduct (Riser)

Project number	GB-BD-002
Date	25-09-2026
Muhammad Sabiq Almuttaqin	
Checked by	Checker
E-201	
Scale	1 : 75

